



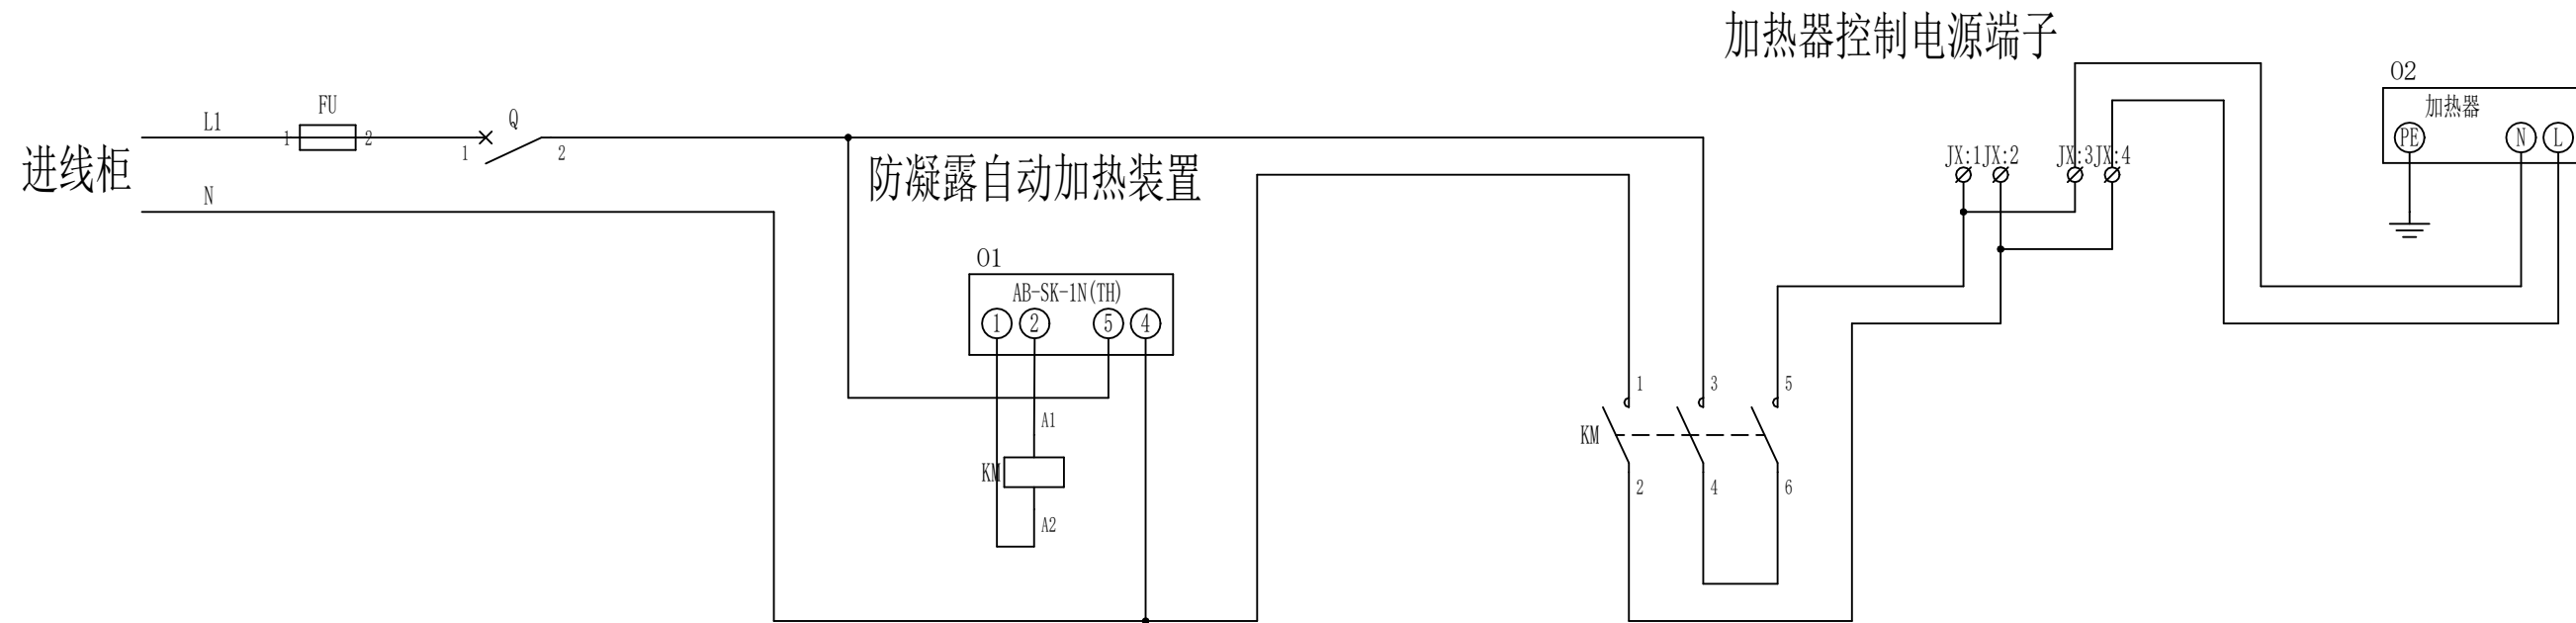


适用于进线柜

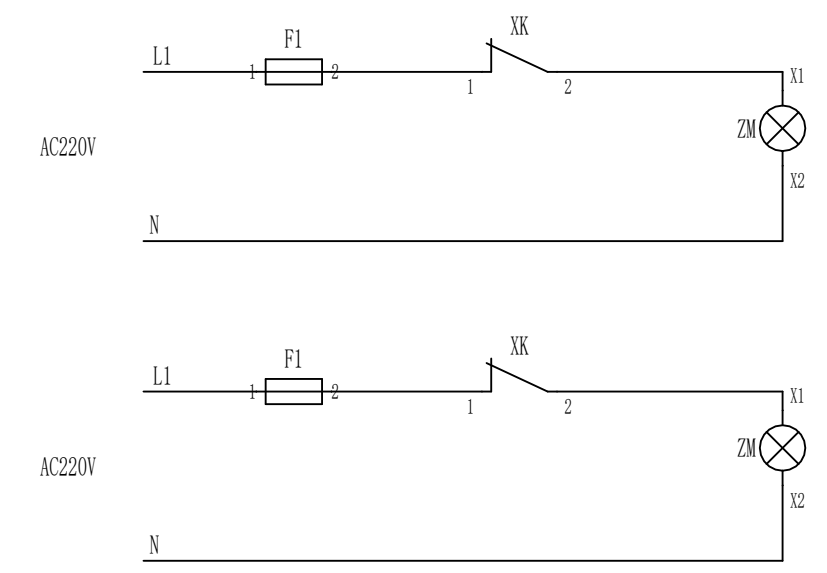


适用于所有环控柜

接主母排A相 N相

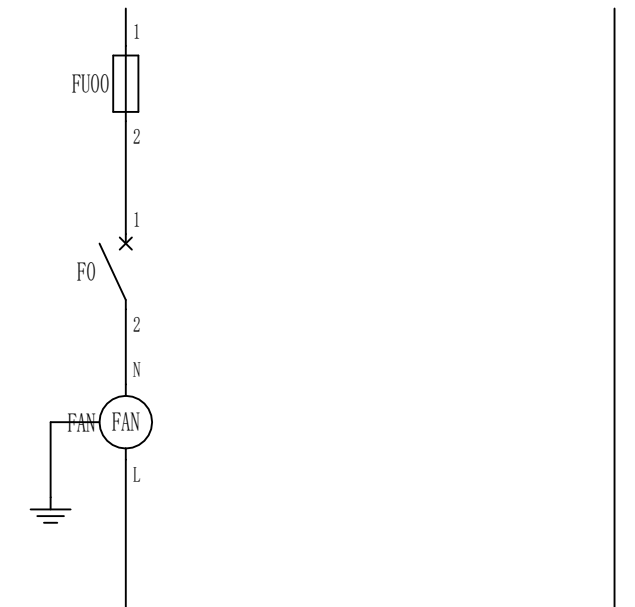

此图用于除变频、软启、PLC柜以外接FU9803风扇的图纸

设计	白立红	日期	2025. 5. 8	客户名称				合同号	A17387		
校对	杨鹏	日期	2025. 5. 8	工程名称	成都轨道交通18号线工程			版本号			
审核	杨鹏	日期	2025. 5. 8	系统名称				图纸名称	加热器原理图	共 2 页	
								原理图号	DZ-24-7	第 1 页	

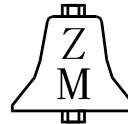

镇江默勒电器有限公司
Zhenjiang Klockner-Moeller