




进线柜

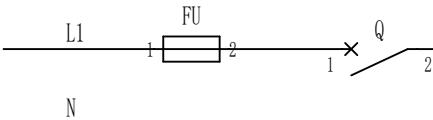

防凝露自动加热装置

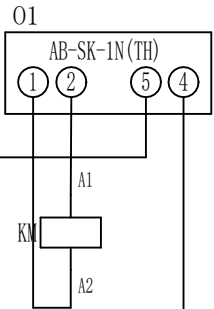


加热器控制电源端子

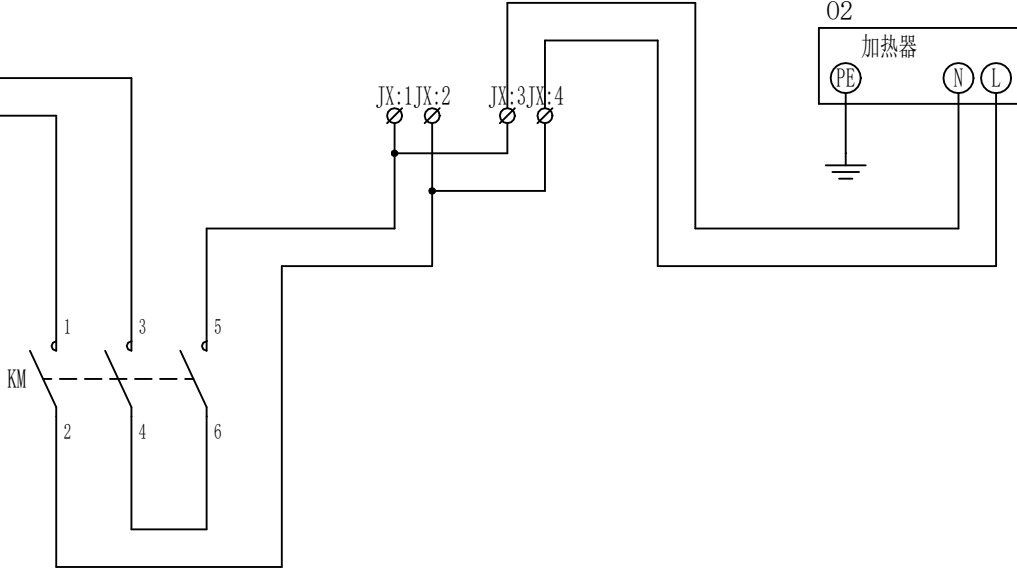


适用于进线柜

AC220V

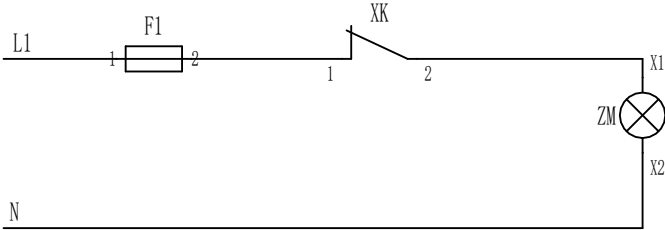


接主母排A相

N相

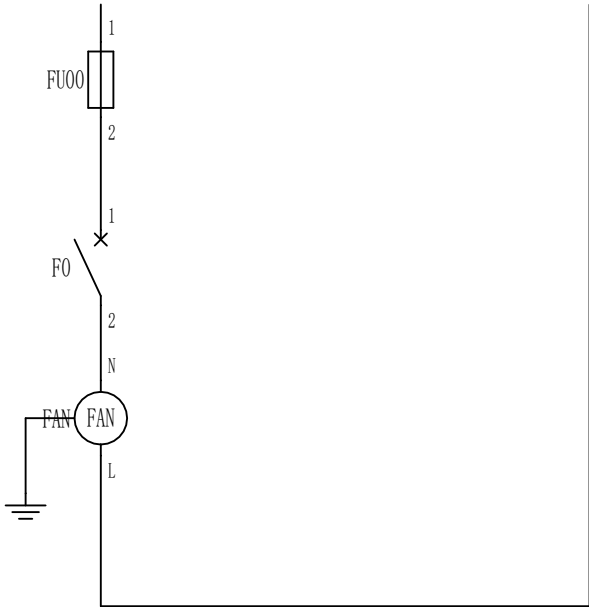

此图用于除变频、软启、PLC柜以外接FU9803风扇的图纸

适用于所有环控柜

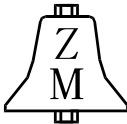设计	白立红	日期	2026. 5. 8	客户名称	 镇江默勒电器有限公司 Zhenjiang Klockner-Moeller	合同号	A17387		
校对	杨鹏	日期	2026. 5. 8	工程名称		成都轨道交通18号线工程	版本号		
审核	杨鹏	日期	2026. 5. 8	系统名称			图纸名称	加热器原理图	共 2 页
							原理图号	DZ-24-6	第 1 页