


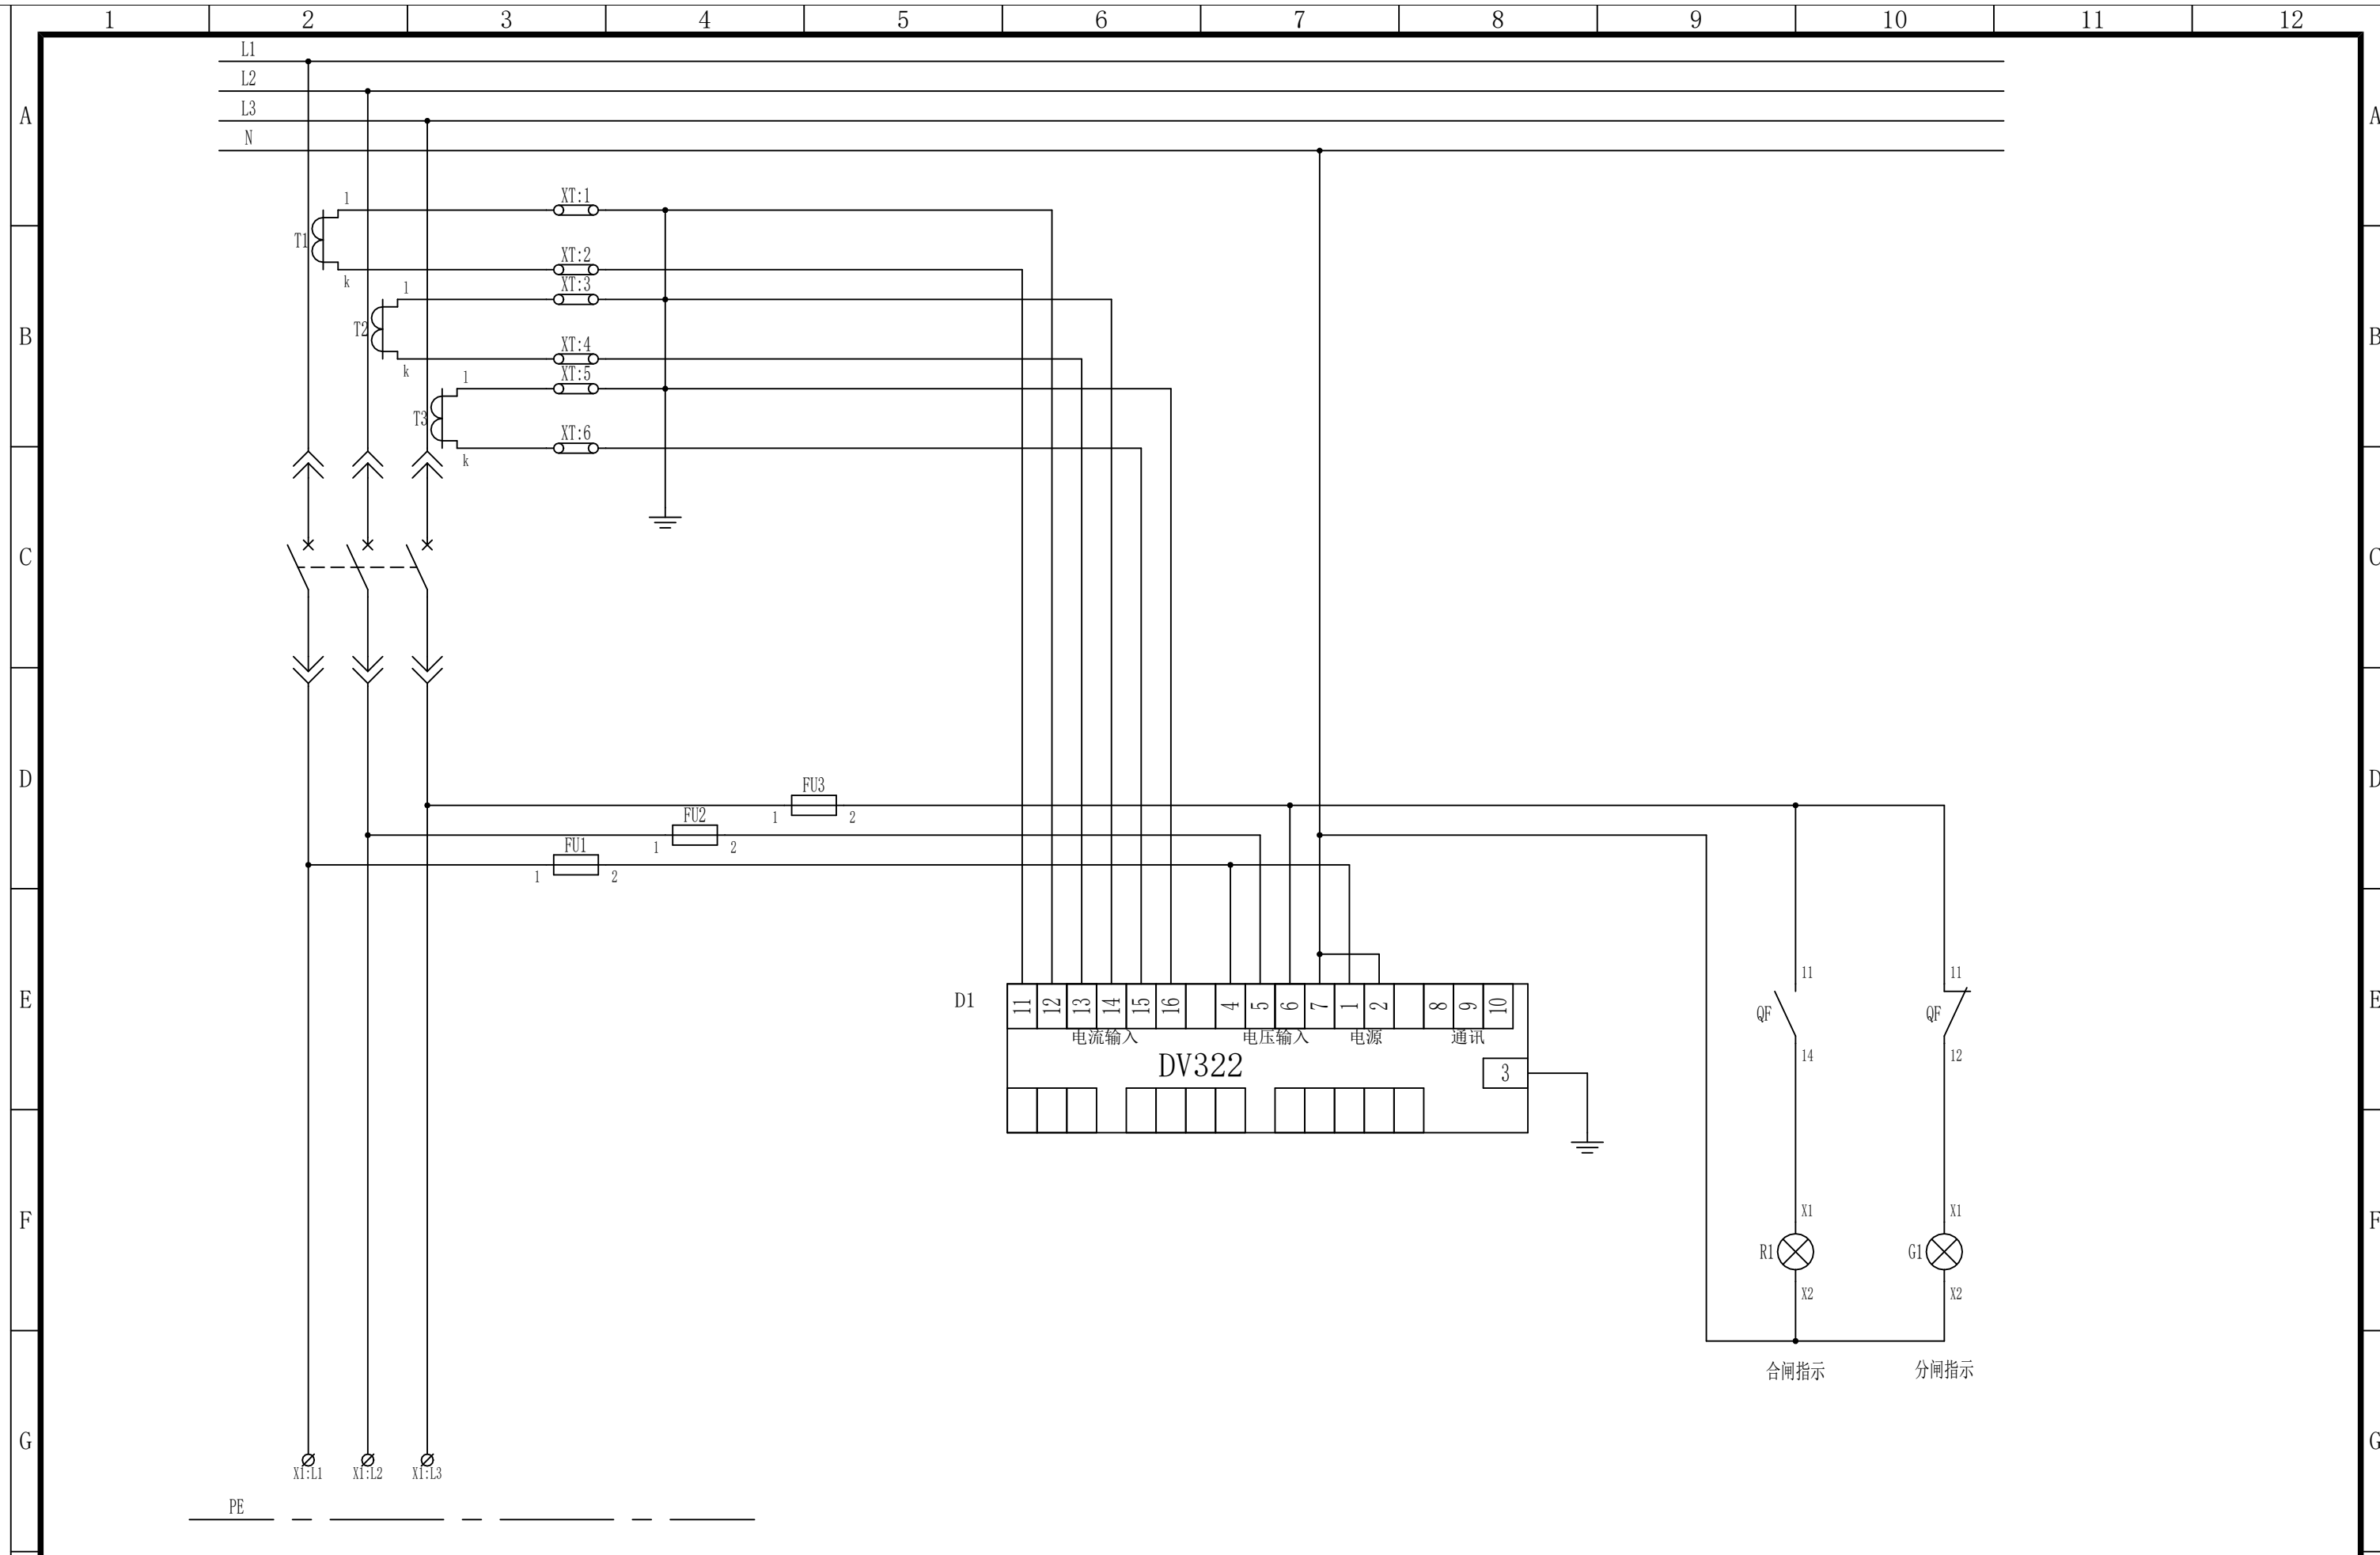

A

B

C

D

E

F

G

H

123456789101112

D1:14

1

T1:l

D1:11

2

T1:k

D1:16

3

T2:l

D1:13

4

T2:k

D1:12

5

T3:l

D1:15

6

T3:k

XT

13	XT附件3	端子（附件）	UZB8横 1-10	1	
12	XT附件1	端子（附件）	D-TB 6-RTK-N	1	
11	XT	一次端子	TB 6-RTK N	6	
10	X01附件4	端子（附件）	UZB6横 11-20	1	
9	X01附件3	端子（附件）	UZB6横 1-10	1	
8	X01附件2, XT附件2	端子（附件）	E/UK	4	
7	X01附件1	端子（附件）	D-TB4/10	1	
6	X01	二次端子	TB4I	5	
5	R1	指示灯	AD16-22D/r31S 红色 AC220V 附：A22-RAS-X(1) + 有机玻璃 1.0 *26mm*8mm无背胶(1)	1	合闸指示
4	G1	指示灯	AD16-22D/g31S 绿色 AC220V 附：A22-RAS-X(1) + 有机玻璃 1.0 *26mm*8mm无背胶(1)	1	分闸指示
3	FU1, FU2, FU3	低压熔断器（附件）	NRT18-32X 附：NRT18-32 6A(1)	3	
2	X1		详见一次系统图	3	
1	D1, QF, T1, T2, T3		详见一次系统图	5	
序号	代号	元件名称	规格型号	数量	备注

设计	白立仁	日期	2024.6.27	客户名称		Z M 镇江默勒电器有限公司 Zhenjiang Klockner-Moeller	合同号	A17387	
校对	杨鹏	日期	2024.6.27	工程名称	成都地铁市轨道交通18号线		版本号		
审核	杨鹏	日期	2024.6.27	系统名称			图纸名称	单电源进线	共 2 页
							原理图号	CDDT-6-DZ-.02	第 2 页

123456789101112