


8	F	微型断路器	S202-D6	1	
7	X01附件3	端子（附件）	UZB6横 1-10	1	
6	X01附件2	端子（附件）	E/UK	2	
5	X01附件1	端子（附件）	D-TB4/10	1	
4	X01	二次端子	TB4I	10	
3	R1	指示灯	AD16-22D/r31S 红色 AC220V 附：有机玻璃 1.0*26mm*8mm无背胶(1) + A22-RAS-X(1)	1	电源指示
2	FU	低压熔断器（附件）	NRT18-32X 附：NRT18-32 6A(1)	1	
1	S1	按钮	LA39-B3-11X/k 黑色 附：A22-RAS-X(1) + 有机玻璃 26*8mm A22-XA(停止 启动) (1)	1	
序号	代号	元件名称	规格型号	数量	备注

X01			
R1:X1	1		
	2		
R1:X2	3	N	
	4		
	5	PE	
	6		
	7		
	8		
	9		
	10		

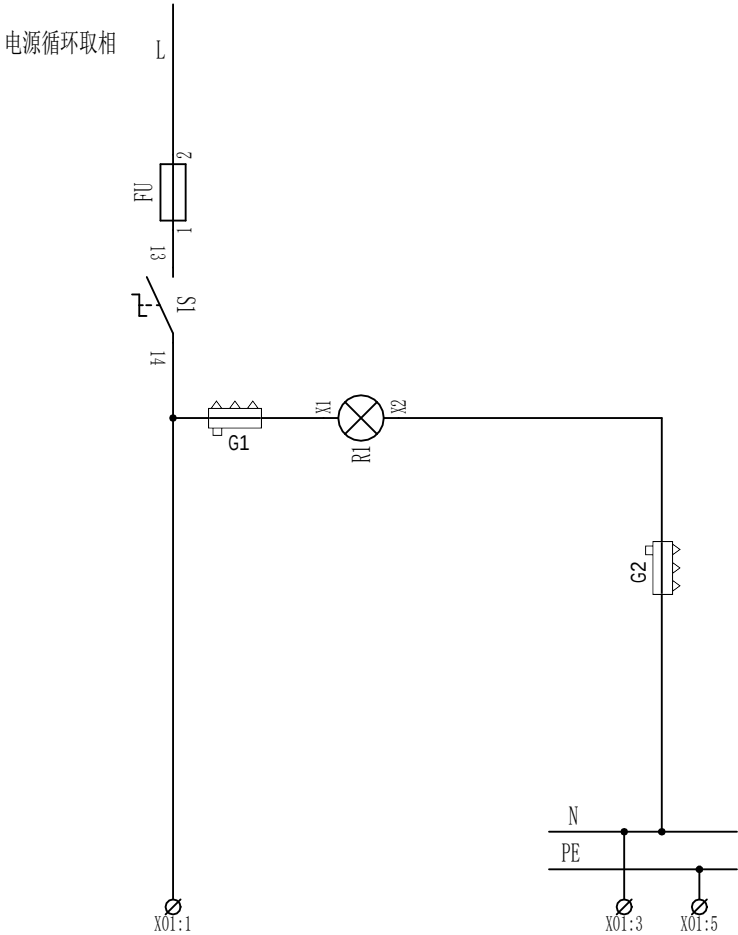

电源指示
显示

设计	白立红	日期	2024.6.27	客户名称	
校对	杨鹏	日期	2024.6.27	工程名称	成都轨道交通18号线工程
审核	杨鹏	日期	2024.6.27	系统名称	



镇江默勒电器有限公司
Zhenjiang Klockner-Moeller

合同号	A17387		
版本号			
图纸名称	电动蝶阀控制原理	共	1 页
原理图号	CDDT-6-DZ-.06	第	1 页