



A
B
C
D
E
F
G
H



信号输入				
公共端	自动	开阀	关阀	就地/手动开关阀

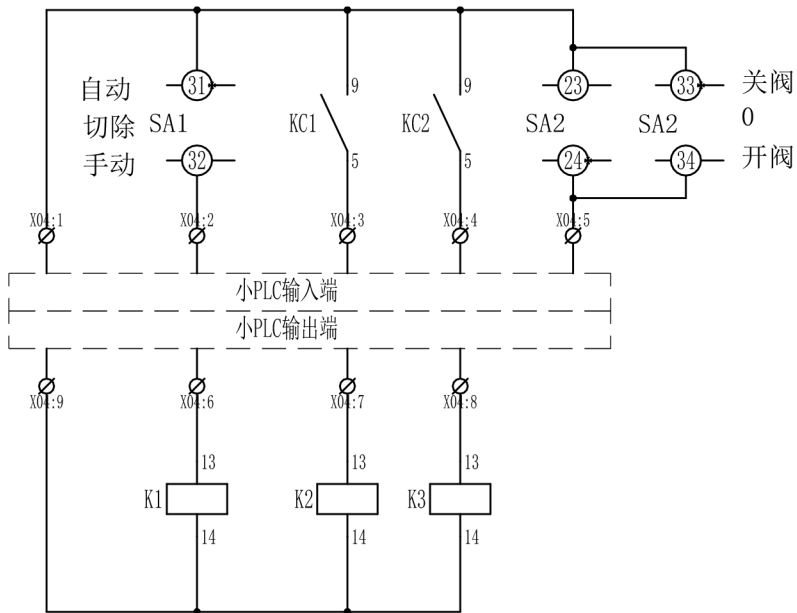

公共端	开阀	关阀	故障报警
控制输出			

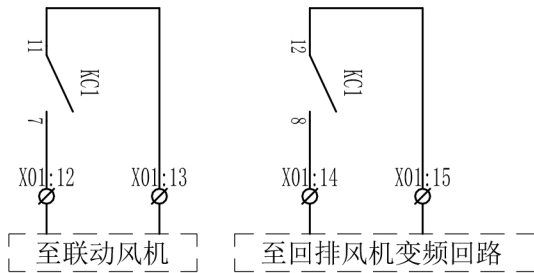

控制方式			
PLC(关阀)	环控(关阀)	PLC(开阀)	环控(开阀)

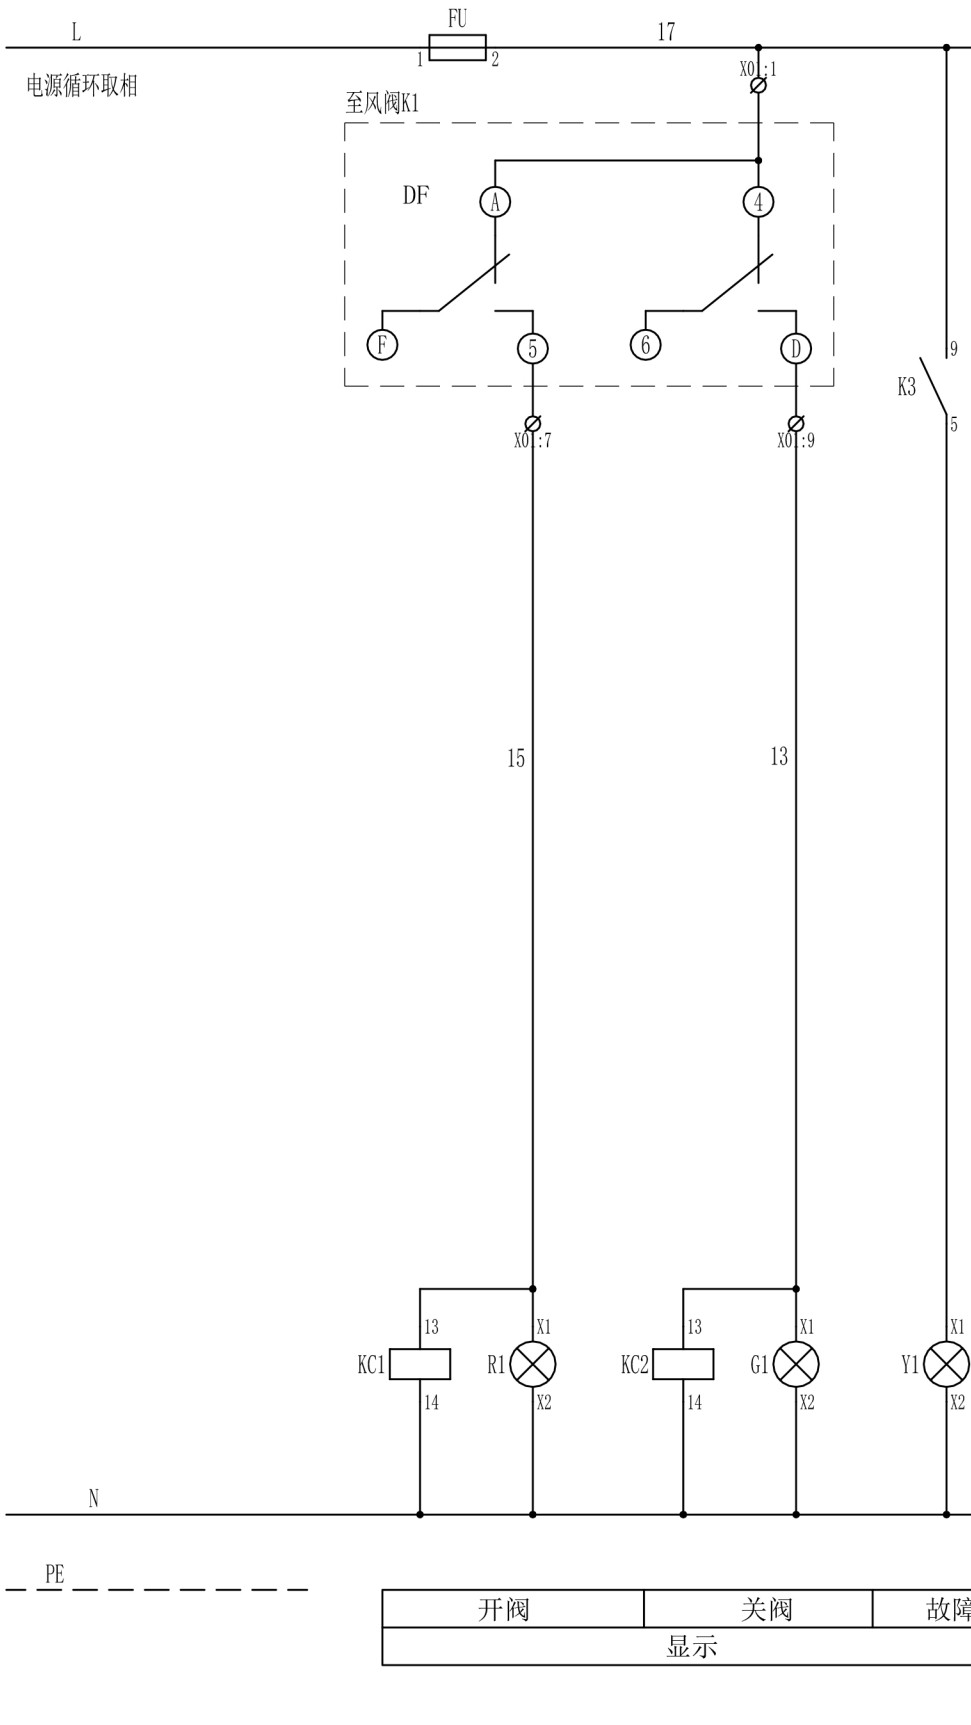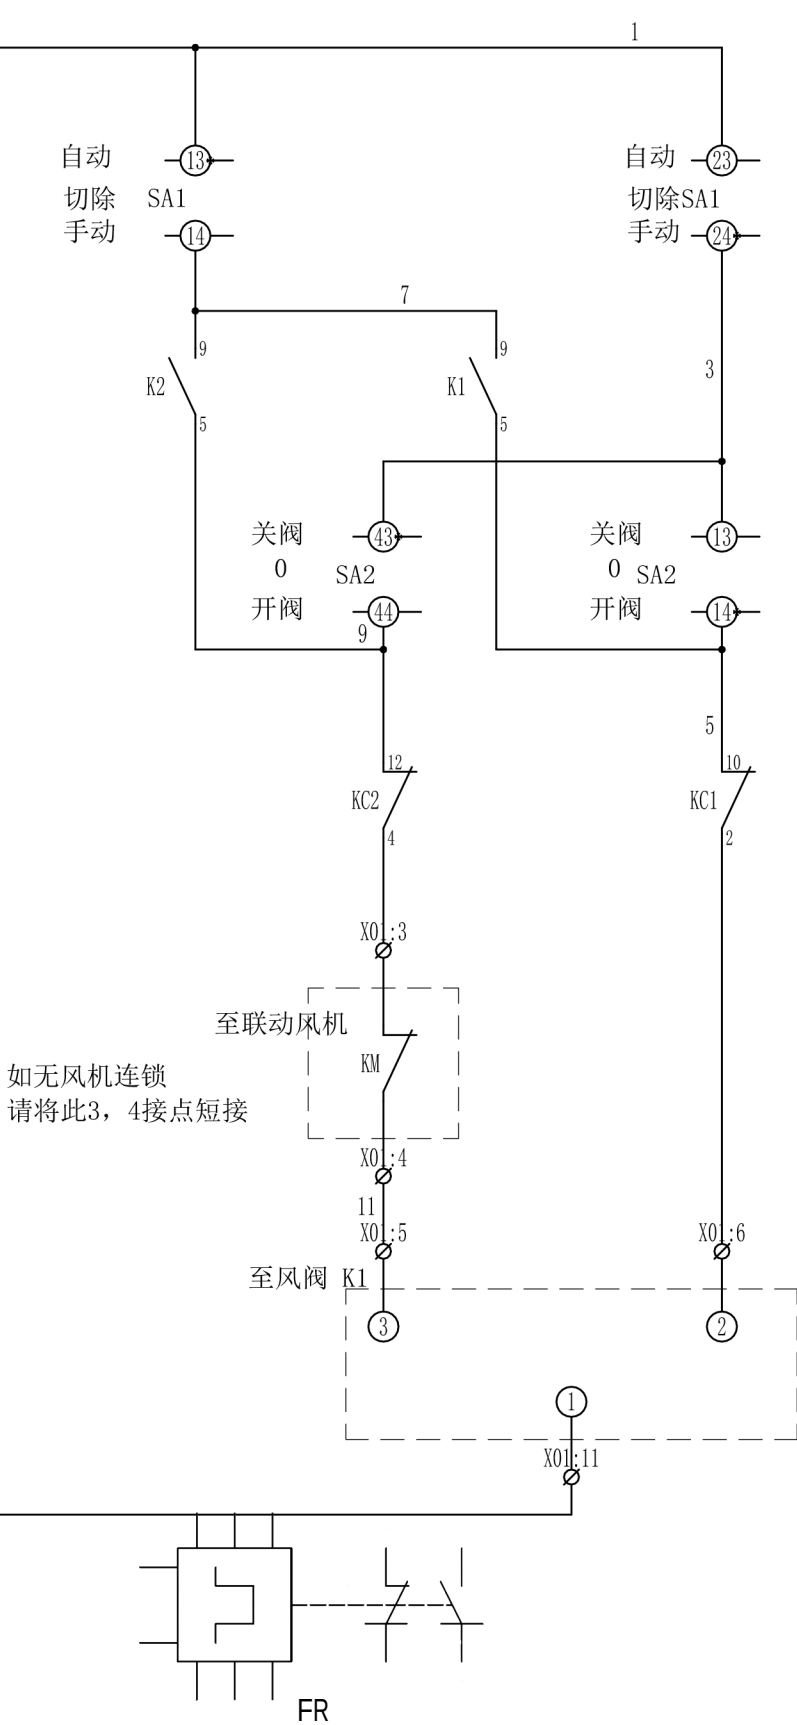

开阀	关阀	故障
显示		

设计	日期	2024.6.27	客户名称	
校对	日期	2024.6.27	工程名称	成都轨道交通18号线工程
审核	日期	2024.6.27	系统名称	



镇江默勒电器有限公司
Zhenjiang Klockner-Moeller

合同号	A17387	
版本号		
图纸名称	组合式风阀MD	共 2 页
原理图号	CDDT-6-DZ-.07	第 1 页