

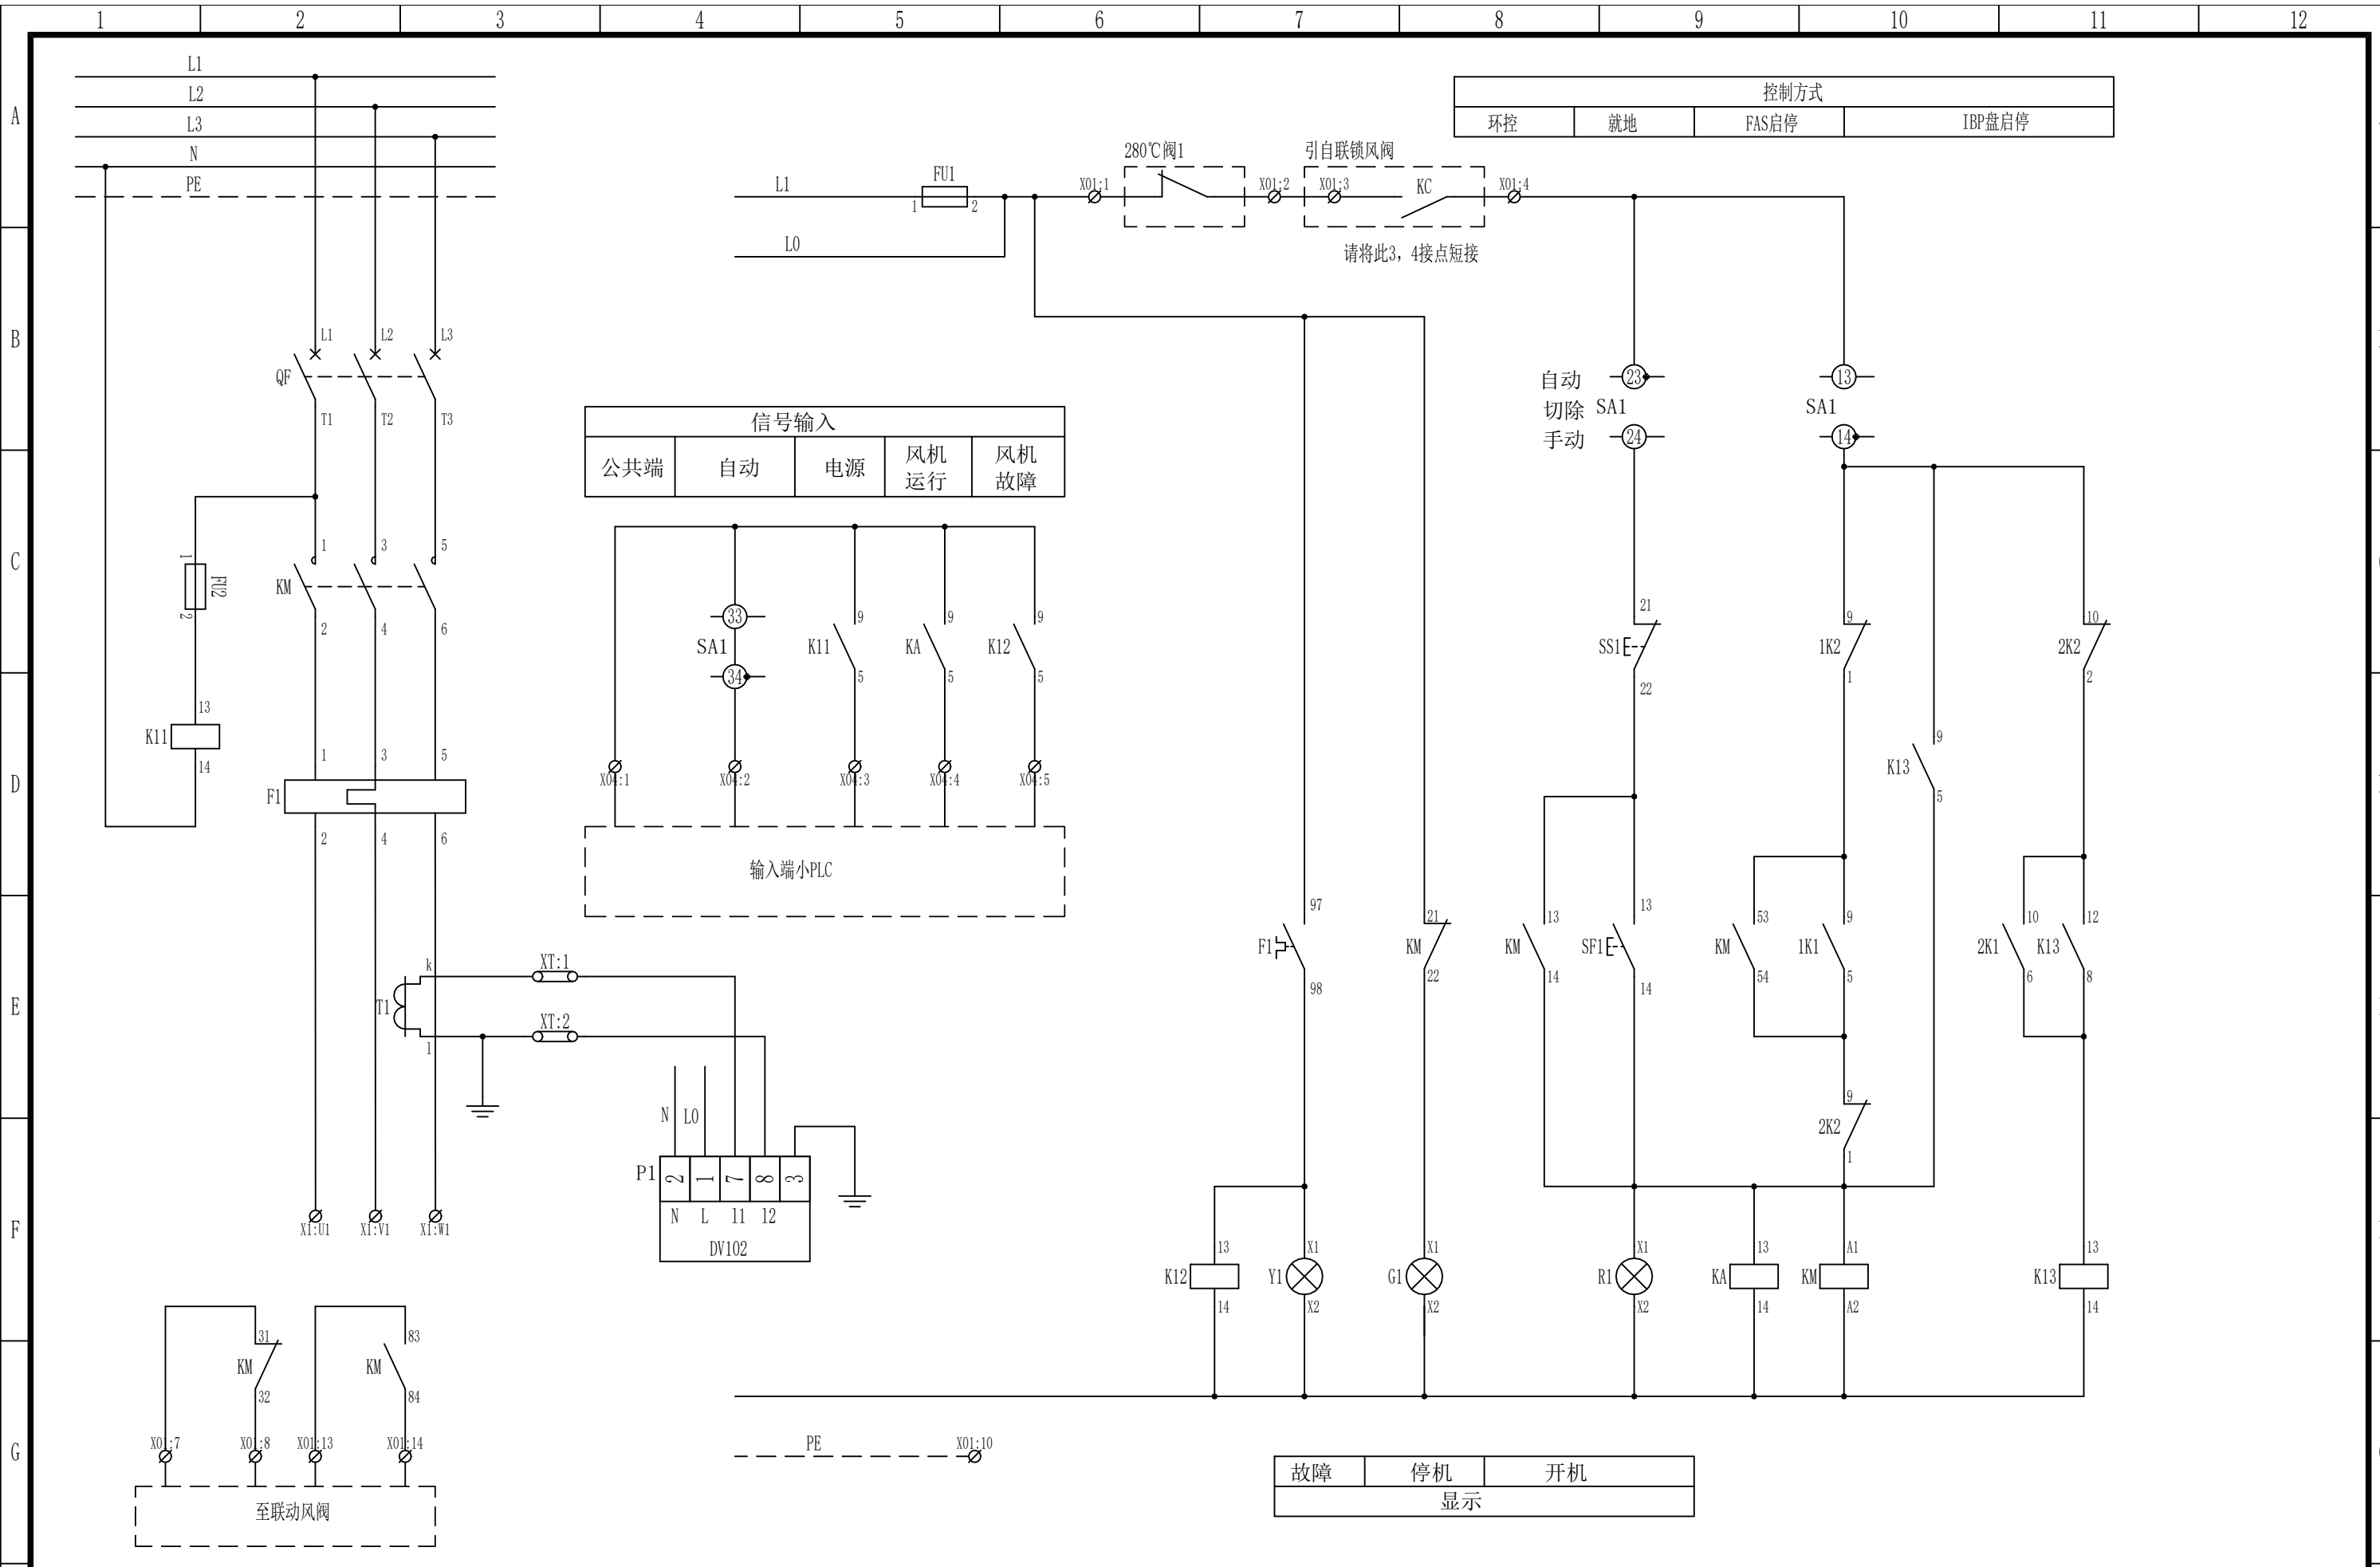


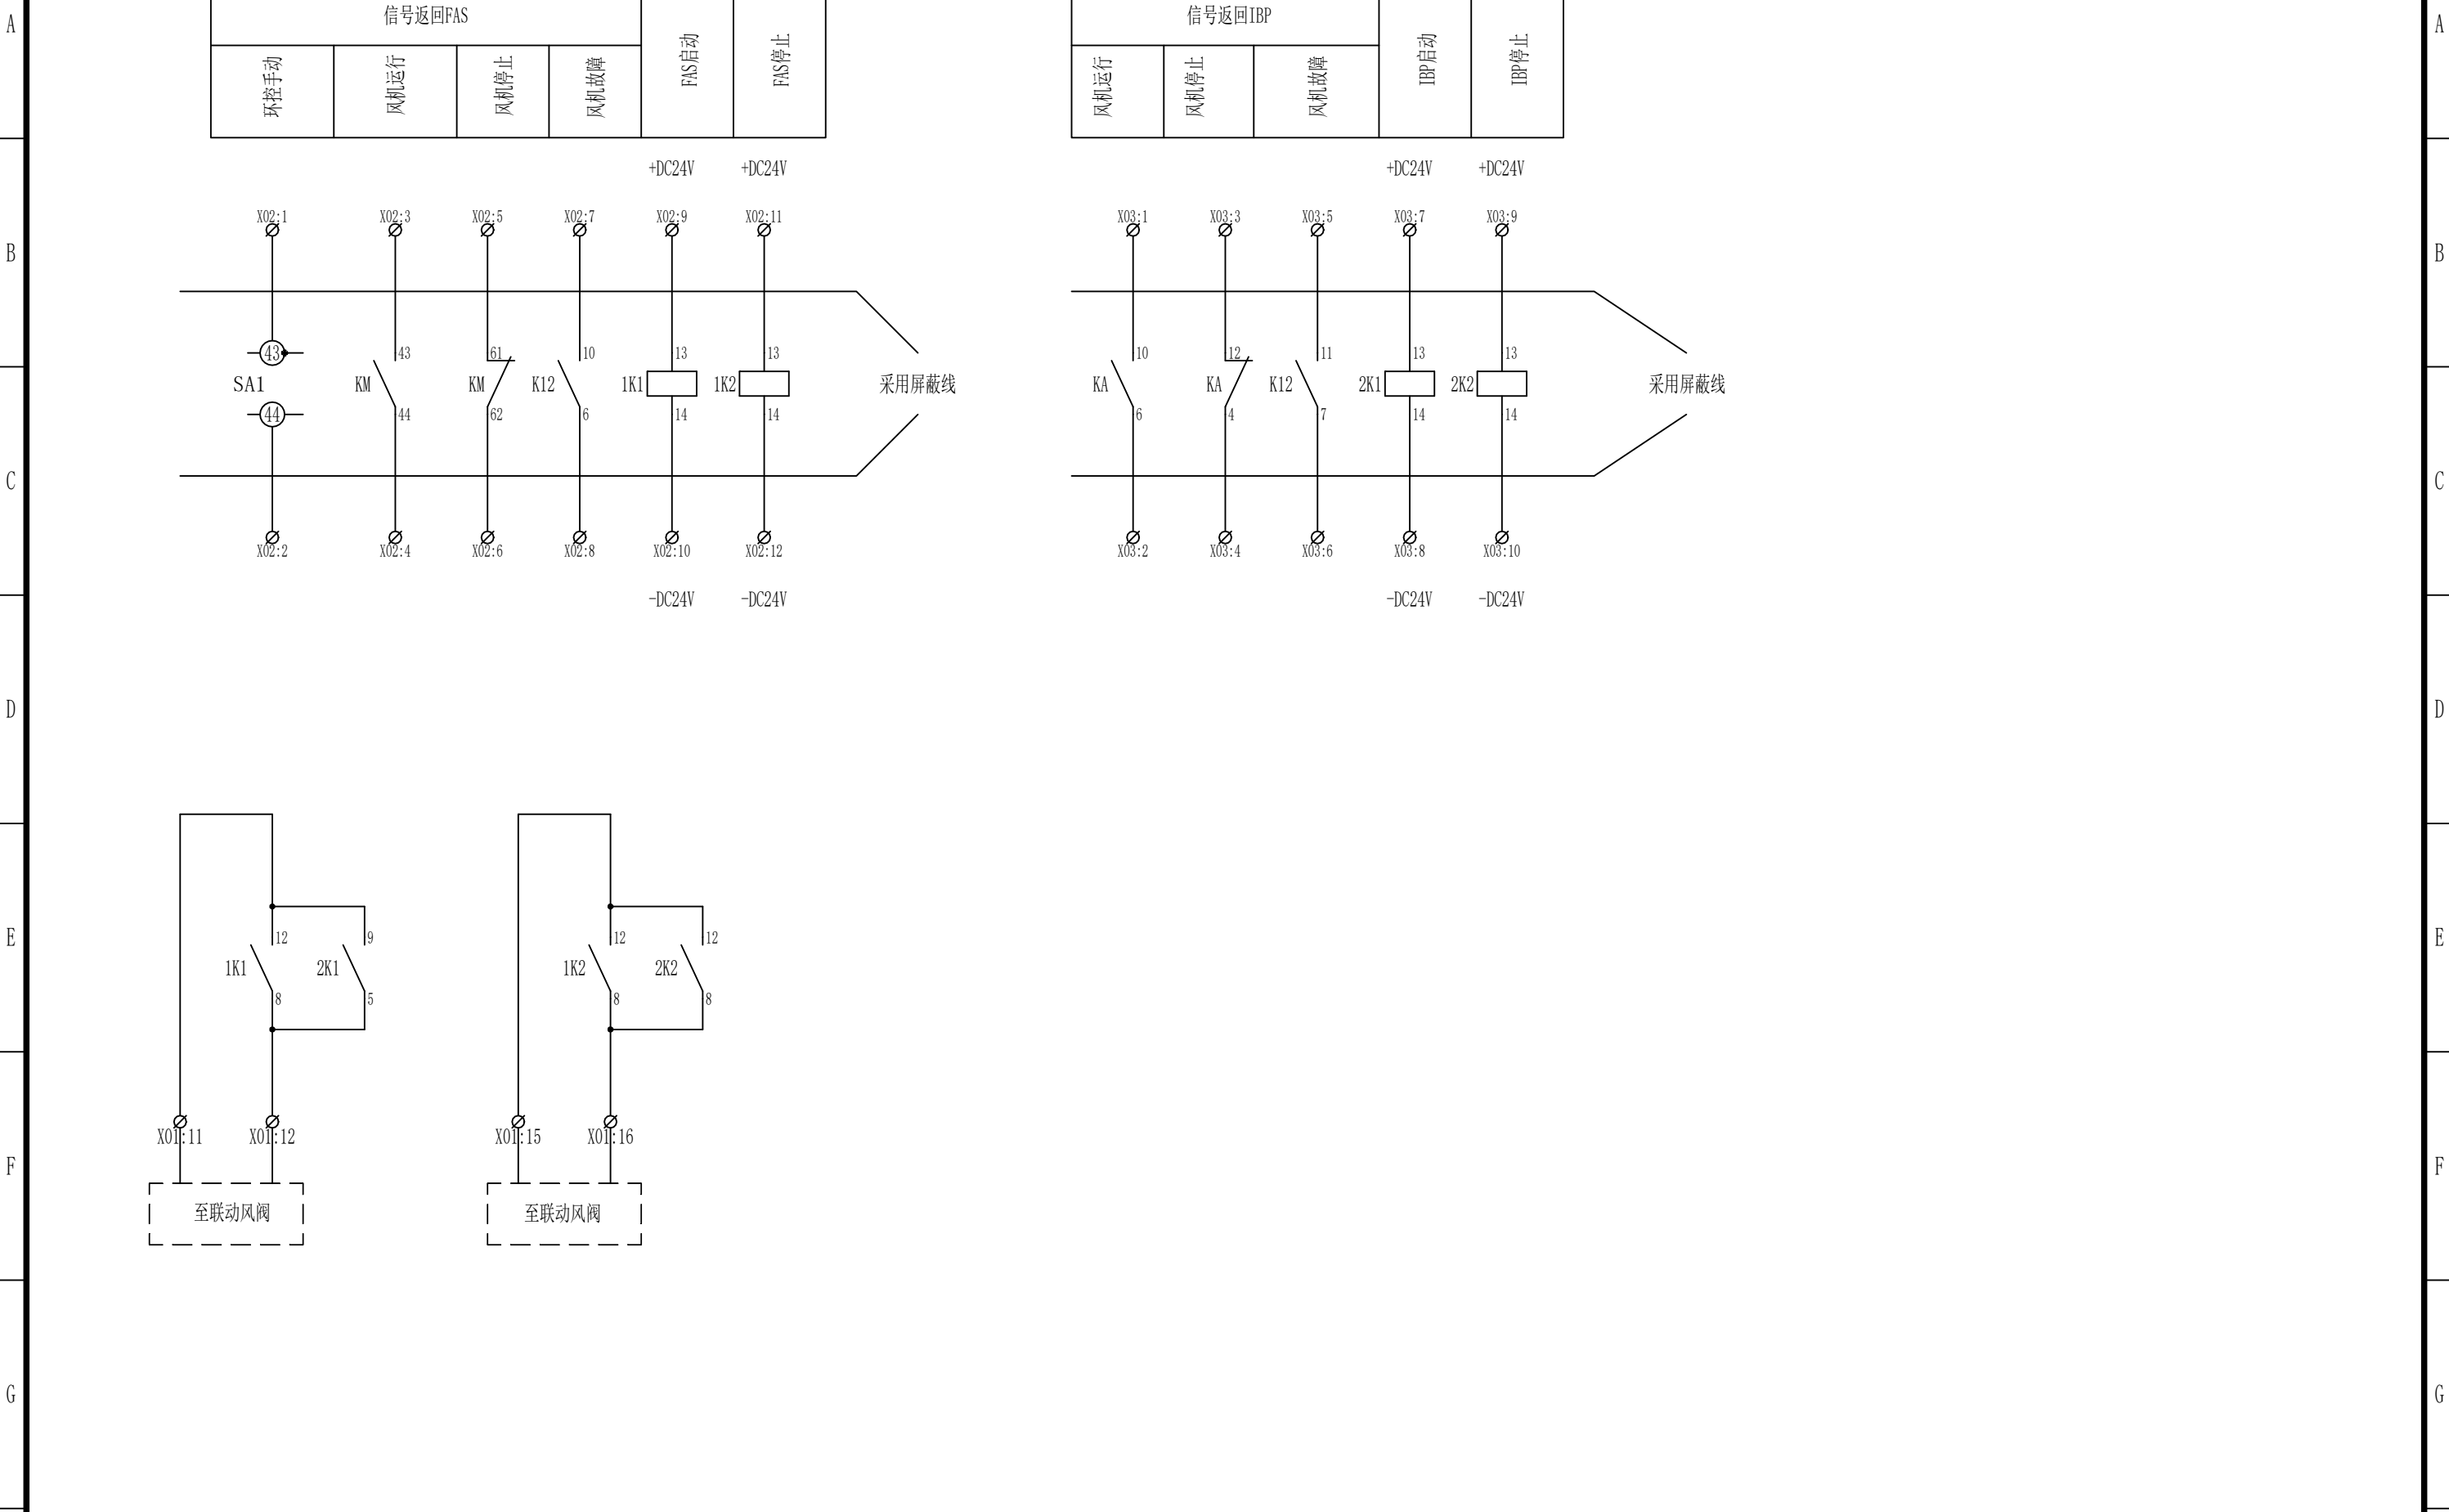

H	设计	白立红	日期	2024.6.27	客户名称				合同号	A17387	
	校对	杨鹏	日期	2024.6.27	工程名称	成都轨道交通18号线工程			版本号		
	审核	杨鹏	日期	2024.6.27	系统名称				图纸名称	专用排烟风机控制原理	共 3 页
									原理图号	CDDT-6-DZ-.10	第 1 页

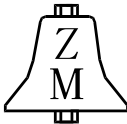

设计	白立红	日期	2024.6.27	客户名称	 镇江默勒电器有限公司 Zhenjiang Klockner-Moeller	合同号	A17387		
校对	杨鹏	日期	2024.6.27	工程名称		成都轨道交通18号线工程	版本号		
审核	杨鹏	日期	2024.6.27	系统名称			图纸名称	专用排烟风机控制原理	共 3 页
						原理图号	CDDT-6-DZ-.10	第 2 页	

A <
--