
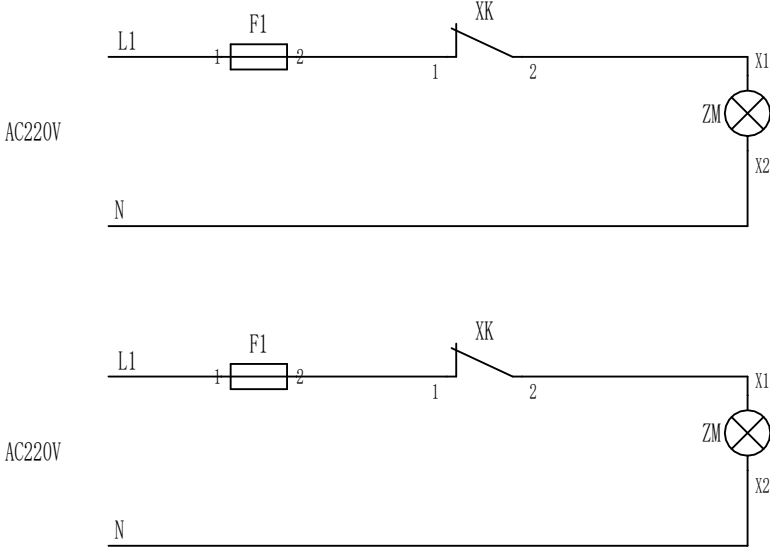


适用于网关柜


适用于所有环控柜


加热器控制电源端子

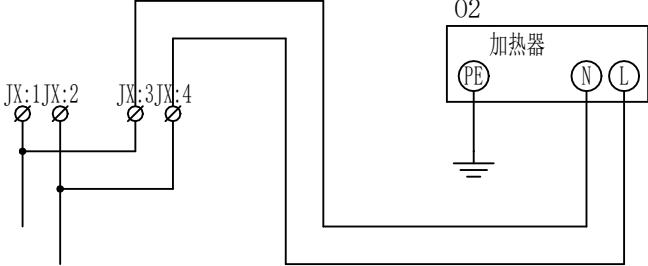

接主母排A相


N相

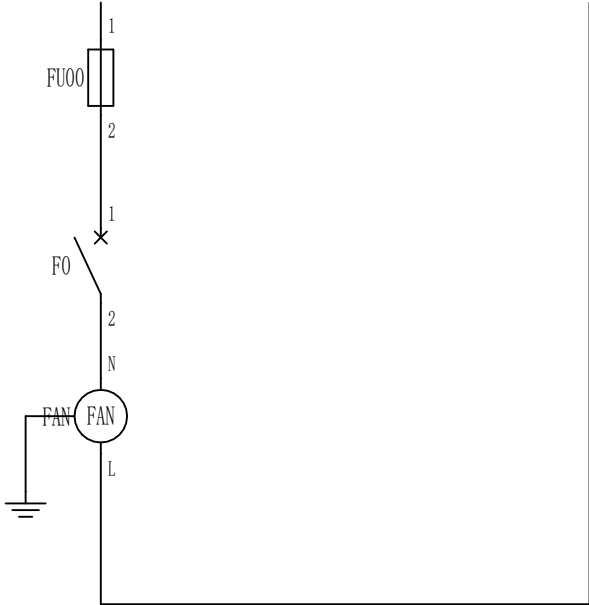

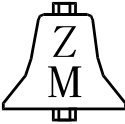H	设计	白立红	日期	2024.6.27	客户名称	 镇江默勒电器有限公司 Zhenjiang Klockner-Moeller			合同号	A17387		
	校对	杨鹏	日期	2024.6.27	工程名称				版本号			
	审核	杨鹏	日期	2024.6.27	系统名称				图纸名称	加热器原理图		共 2 页
									原理图号	CCDT-6-DZ-24-3		第 1 页

A												
B												
C												
D												
	E											
F												
	G											
H												

11	F0	微型断路器	S201-C6	1	
10	FU00	低压熔断器	NRT18-32 4A 附：NRT18-32X (1)	1	
9	ZM	照明灯	LL10-W 220VAC	2	前后各一个
8	XK	行程开关	JW2A-11H/L	2	前后各一个
7	F1	低压熔断器	NRT18-32 6A 附：NRT18-32X (1)	2	前后各一个
6	JX附件3	端子（附件）	UZB6横 1-10	1	
5	JX附件2	端子（附件）	D-TB4/10	1	
4	JX附件1	端子（附件）	E/UK	1	
3	JX	二次端子	TB4I	5	
2	O2	加热器	DJR11-100W AC220V	1	
1	FAN	风机	FU-9806C (2)	1	
序号	代号	元件名称	规格型号	数量	备注

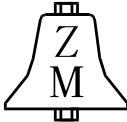设计	白立仁	日期	2024.6.27	客户名称				 镇江默勒电器有限公司 Zhenjiang Klockner-Moeller	合同号	A17387		
校对	杨鹏	日期	2024.6.27	工程名称	成都轨道交通18号线工程				版本号			
审核	杨鹏	日期	2024.6.27	系统名称					图纸名称	加热器原理图	共 2 页	
								原理图号	CCDT-6-DZ-24-3	第 2 页		

1	2	3	4	5	6	7	8	9	10	11	12
---	---	---	---	---	---	---	---	---	----	----	----