



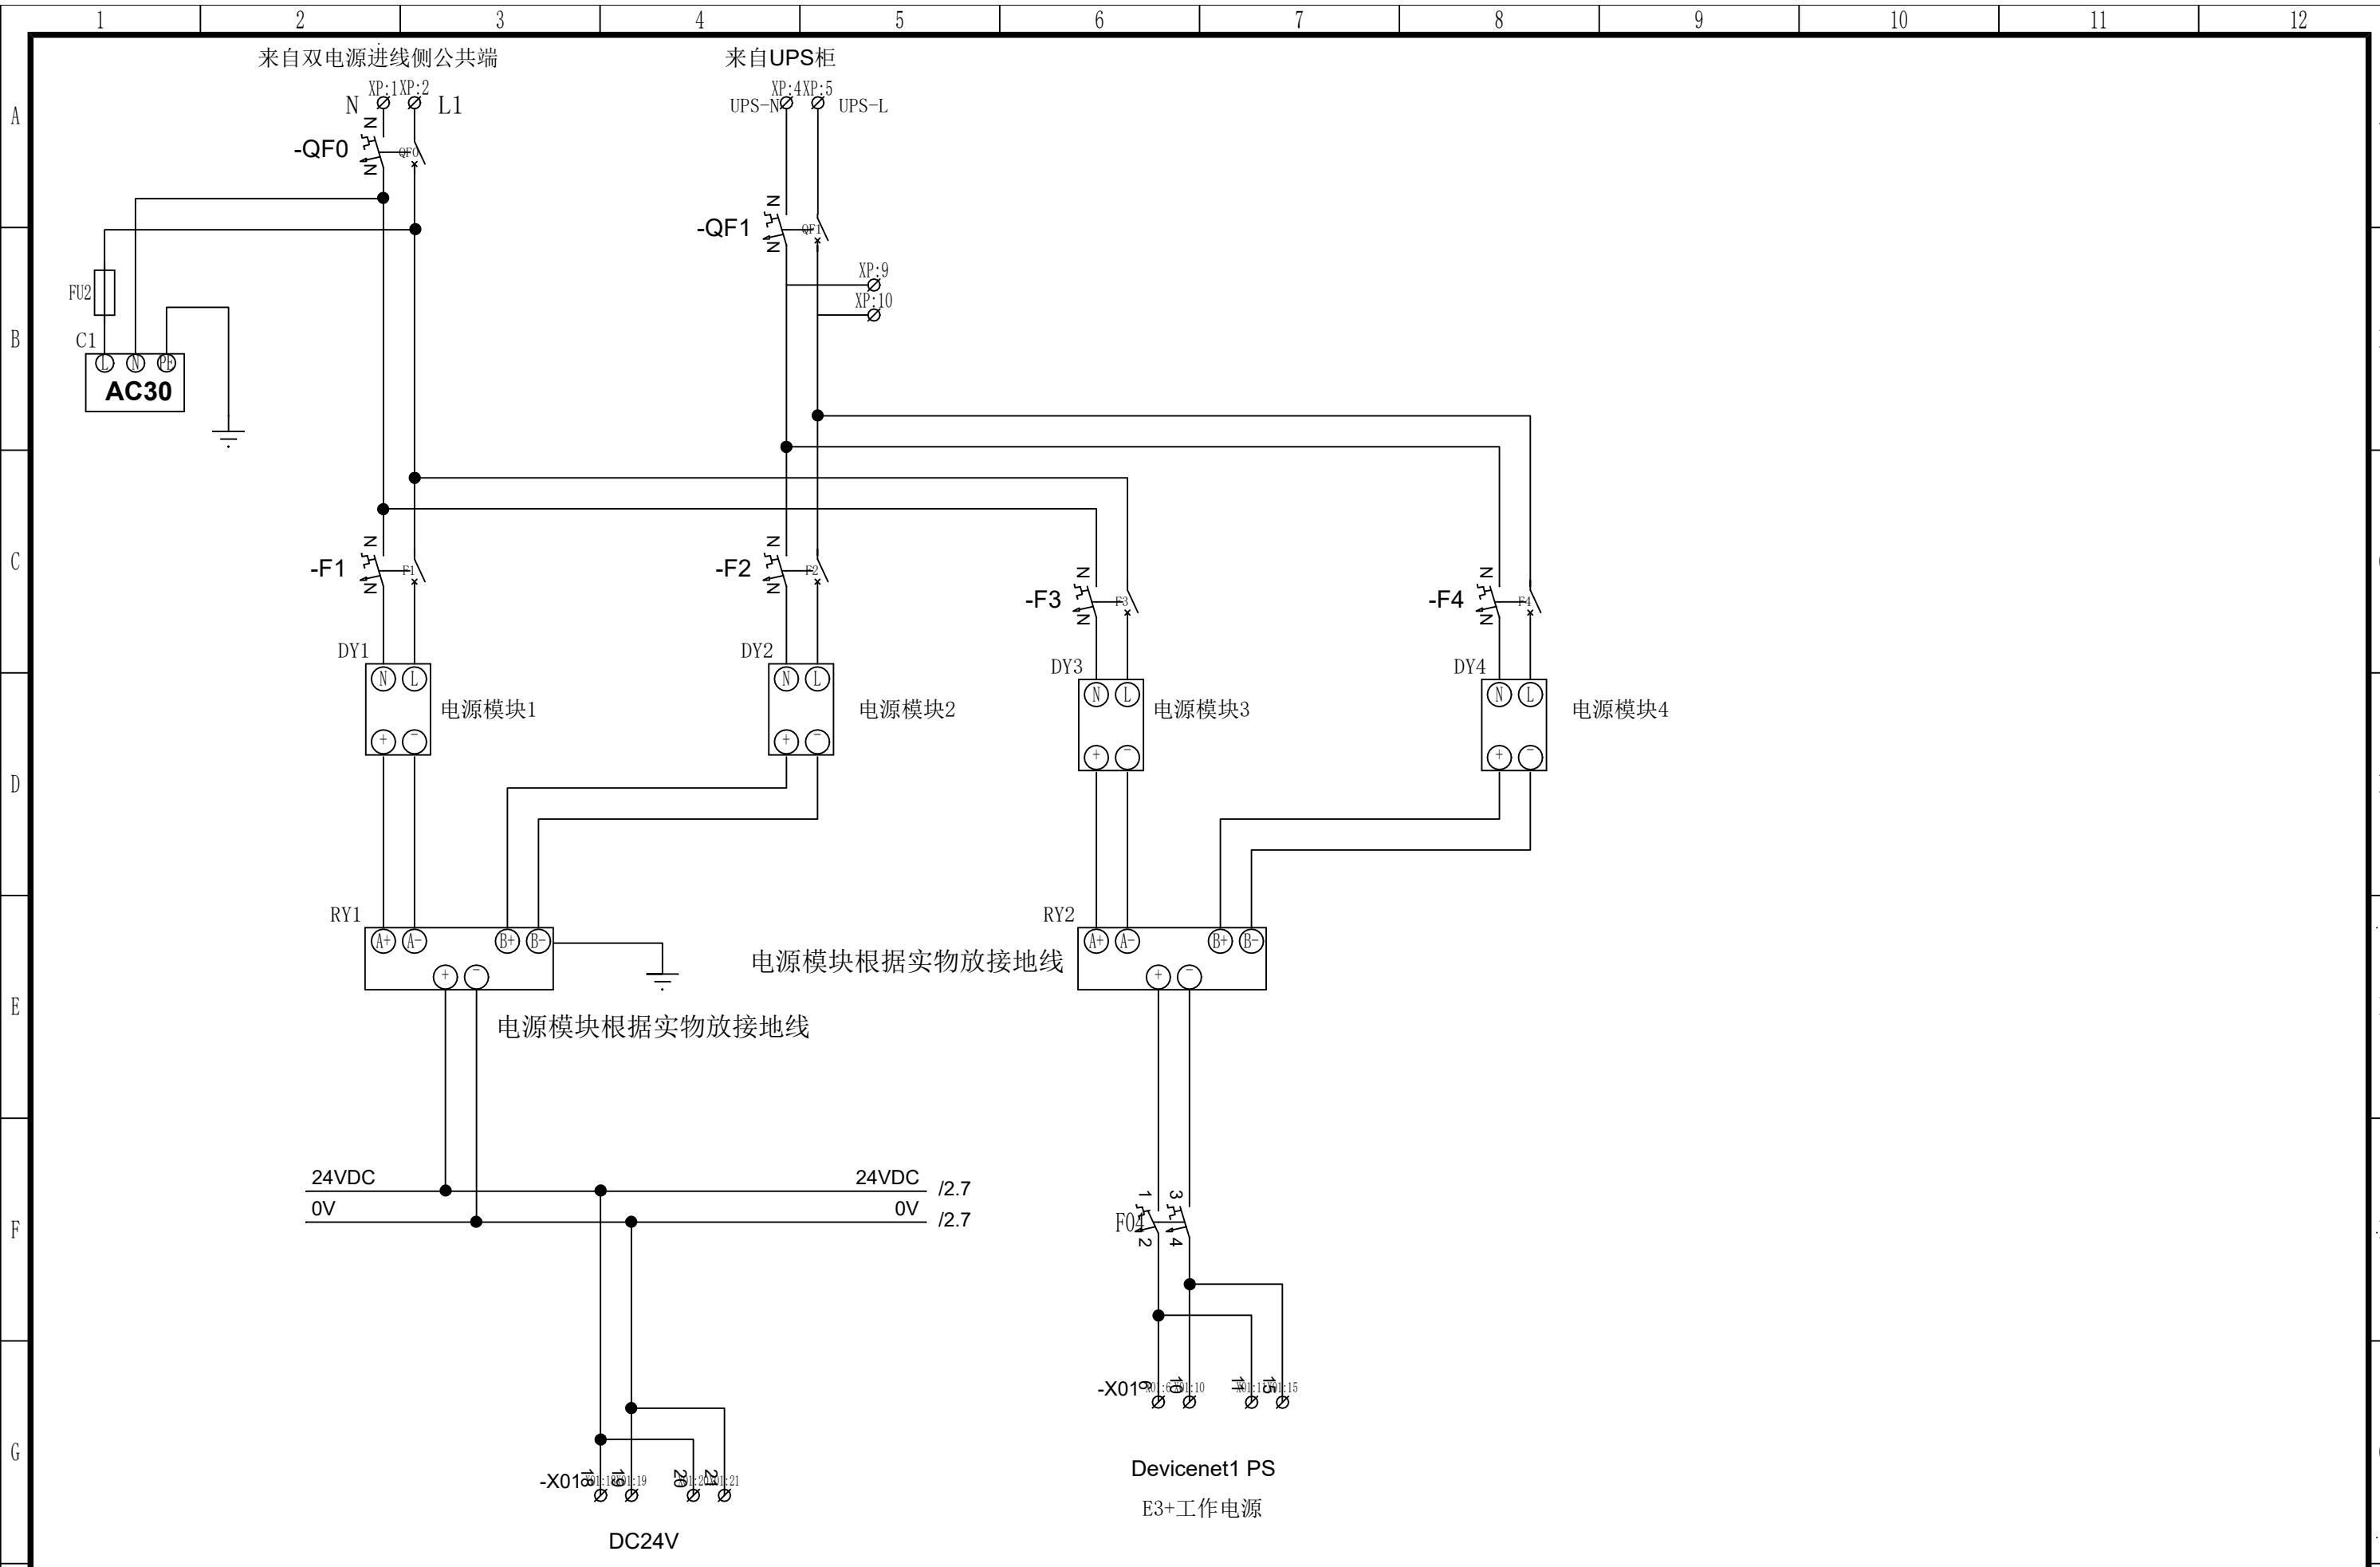

H	设计	白立红	日期	2024.10.14	客户名称				合同号	A17387/1406		
	校对	杨鹏	日期	2024.10.14	工程名称	成都轨道交通18号线工程			版本号			
	审核	杨鹏	日期	2024.10.14	系统名称				图纸名称	网关原理图	共 3 页	
									原理图号	WG-B	第 1 页	

Z
M


镇江默勒电器有限公司
Zhenjiang Klockner-Moeller

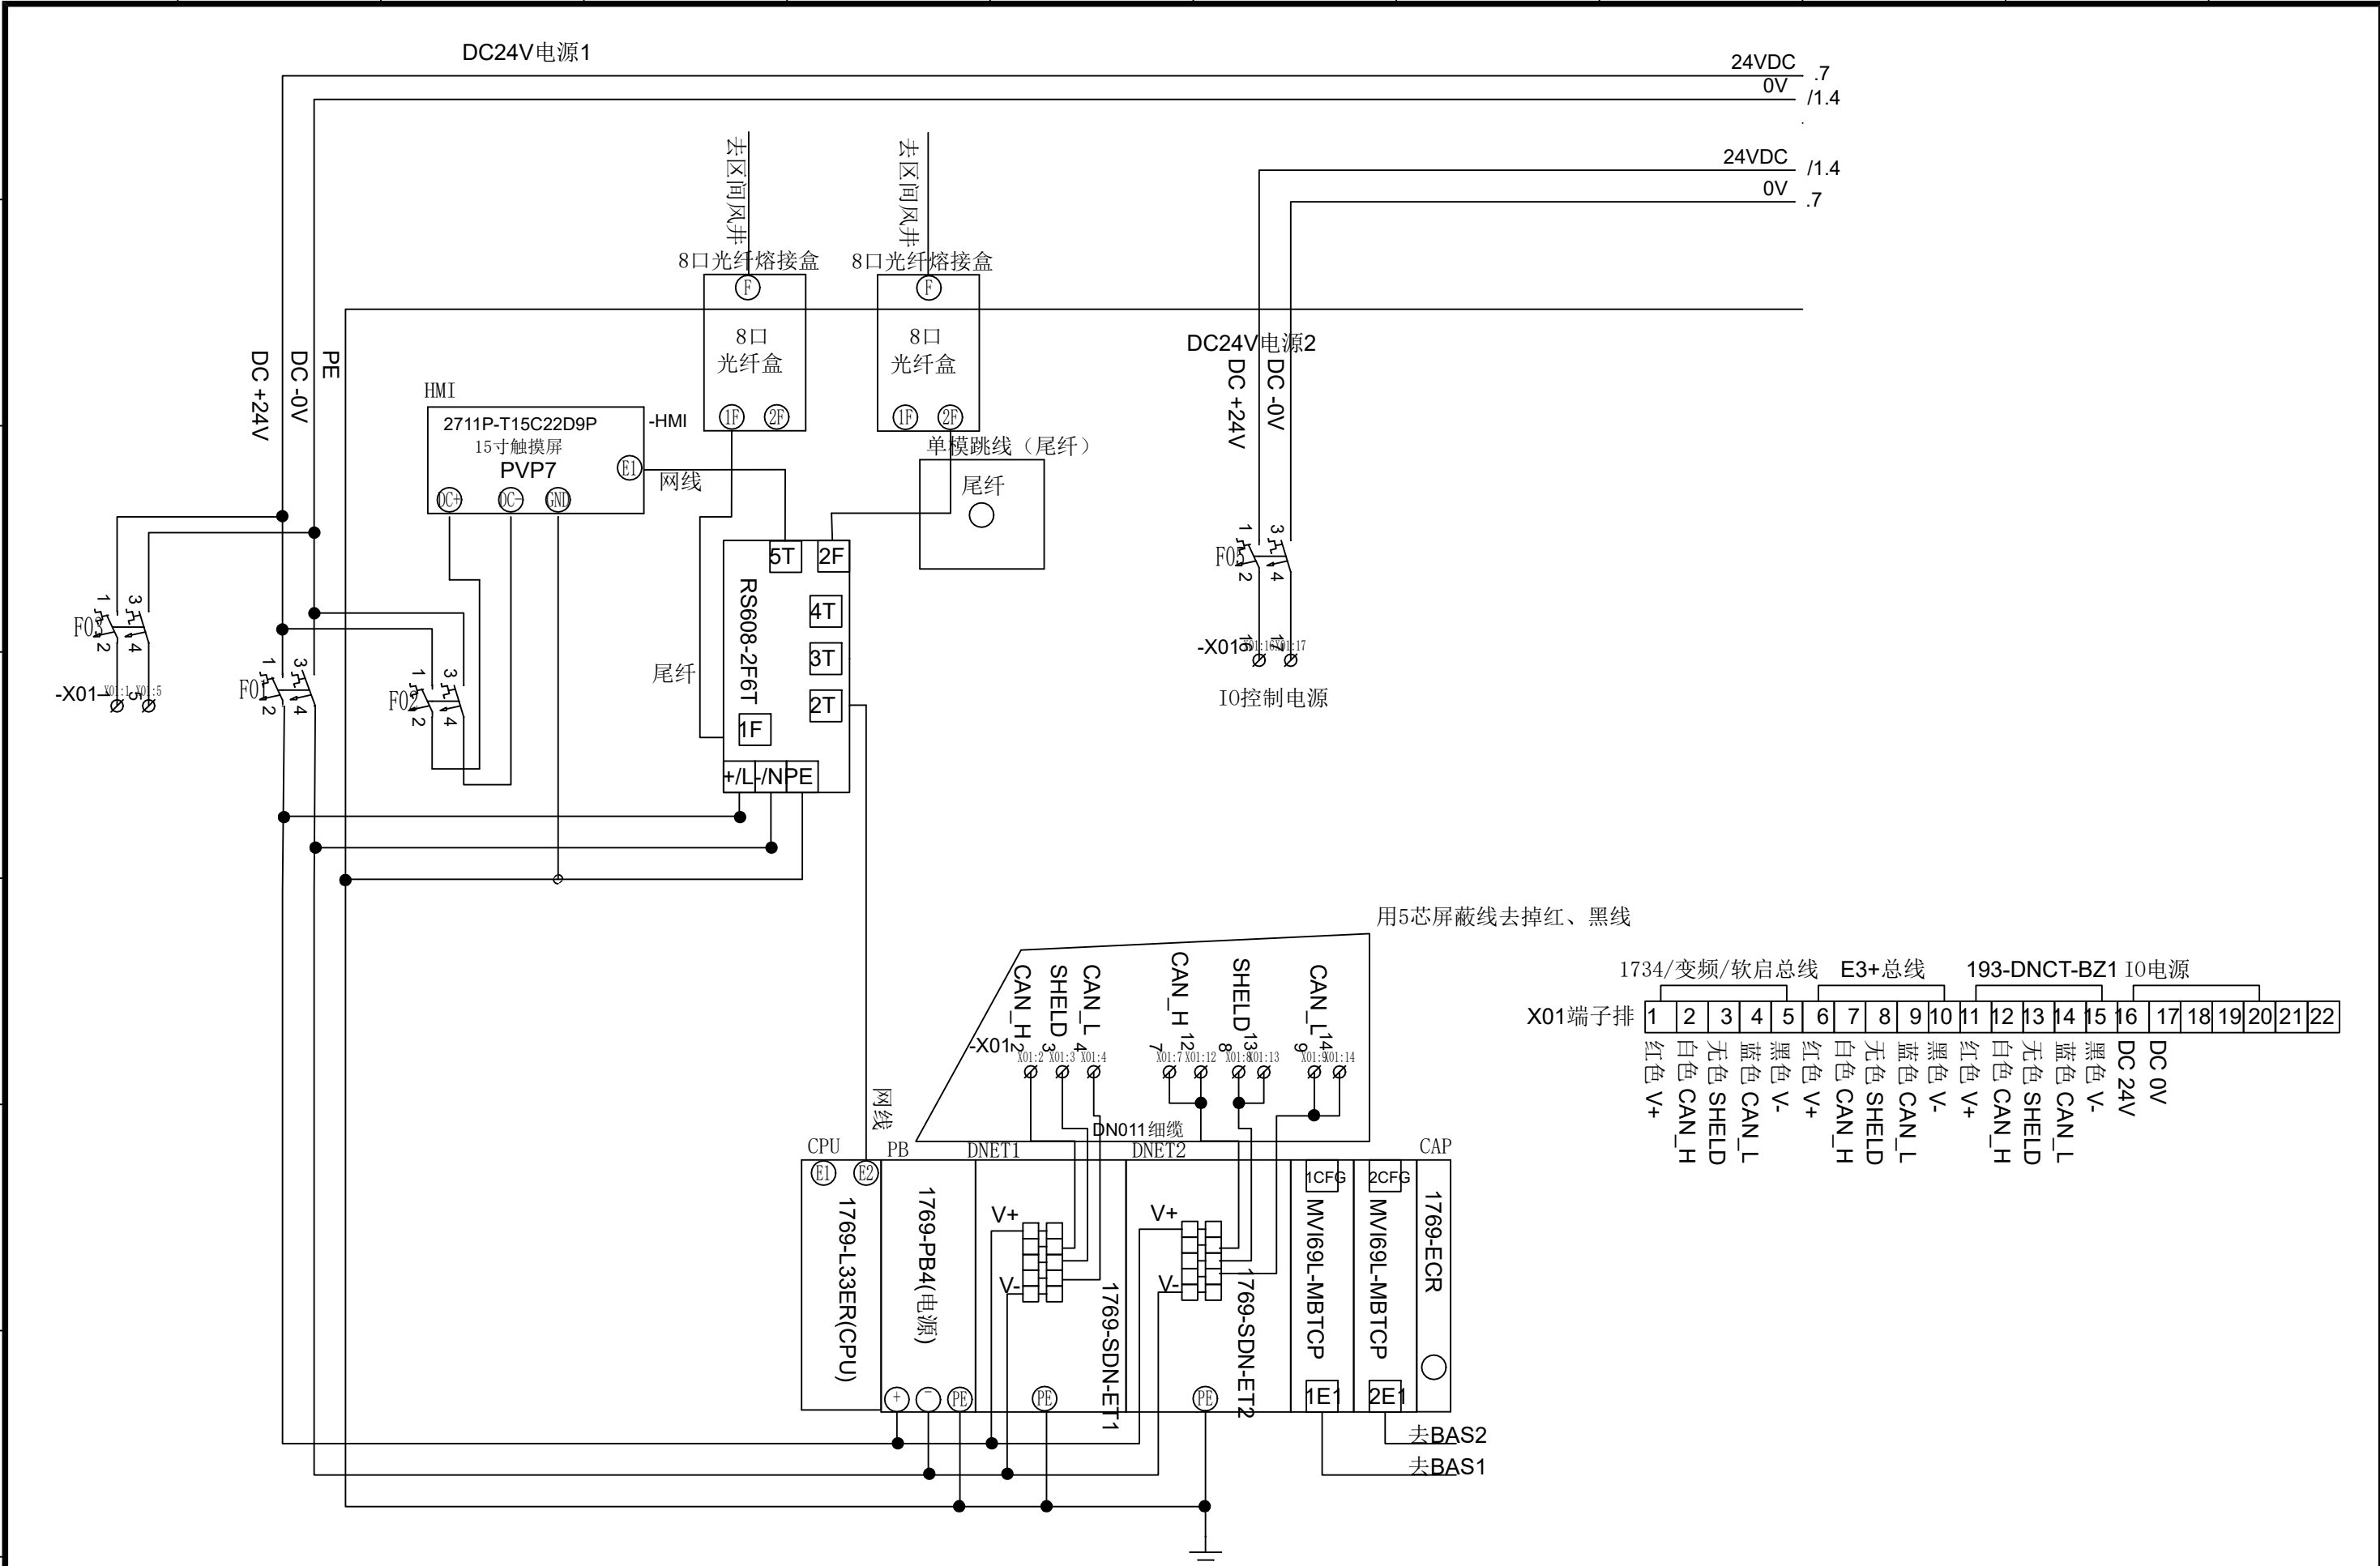

设 计	白红	日 期	2024.10.14	客户名称	 镇江默勒电器有限公司 Zhenjiang Klockner-Moeller	合 同 号	A17387/1406		
校 对	杨鹏	日 期	2024.10.14	工程名称		成都轨道交通18号线工程	版 本 号		
审 核	杨鹏	日 期	2024.10.14	系统名称			图 纸 名 称	网关原理图	共 3 页
							原理图号	WG-B	第 2 页

A												
B												
C												
D												
E												
F												
G												
H												

23	多模跳线（尾纤）	PLC	多模跳线（尾纤） LC-LC-3M/MM	4	
22	光纤盒	PLC	光纤熔接盒	1	
21	JH2	PLC	1783-ETAP2F	1	
20	JH1	PLC	1783-US4T1F	1	
19	X01附件2	端子（附件）	E/UK	4	
18	X01附件1	端子（附件）	D-TB4/10	2	
17	X01附件	端子（附件）	UZB6横 1-10	2	
16	XP附件	端子（附件）	UZB6横 11-20 附：UZB6横 21-30（1）	1	
15	XP	二次端子	TB4I	10	
14	X01	二次端子	TB4I	22	
13	RY1, RY2	电源模块	DRDN20-24	2	
12	DY3, DY4	电源模块	NDR-240-24 输入AC220V/DC24V/10A	2	
11	DY1, DY2	电源模块	SDR-480P-24 输入AC220V/480W/DC24V/20A冗余配置	2	
10	C1	插座	AC30 三插/220V/10A	1	
9	QF0, QF1	微型断路器	S202-C25	2	
8	F01, F02, F03, F04, F05	微型断路器	S202M-C16DC	5	
7	F1, F2, F3, F4	微型断路器	S202-C16	4	
6	FU2	低压熔断器	NRT18-32 6A 附：NRT18-32X（1）	1	
5	PB	PLC	1769-PB4	1	
4	HMI	PLC	2711P-T15C22D9P	1	
3	DNET1, DNET2	PLC	1769-SDN	2	
2	CPU	PLC	1769-L33ER	1	
1	CAP	PLC	1769-ECR	1	
序号	代号	元件名称	规格型号	数量	备注

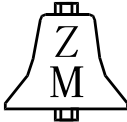设计	白立仁	日期	2024.10.14	客户名称				 镇江默勒电器有限公司 Zhenjiang Klockner-Moeller	合同号	A17387/1406		
校对	杨鹏	日期	2024.10.14	工程名称	成都轨道交通18号线工程				版本号			
审核	杨鹏	日期	2024.10.14	系统名称					图纸名称	网关原理图		共 3 页
								原理图号	WG-B		第 3 页	

1	2	3	4	5	6	7	8	9	10	11	12
---	---	---	---	---	---	---	---	---	----	----	----