


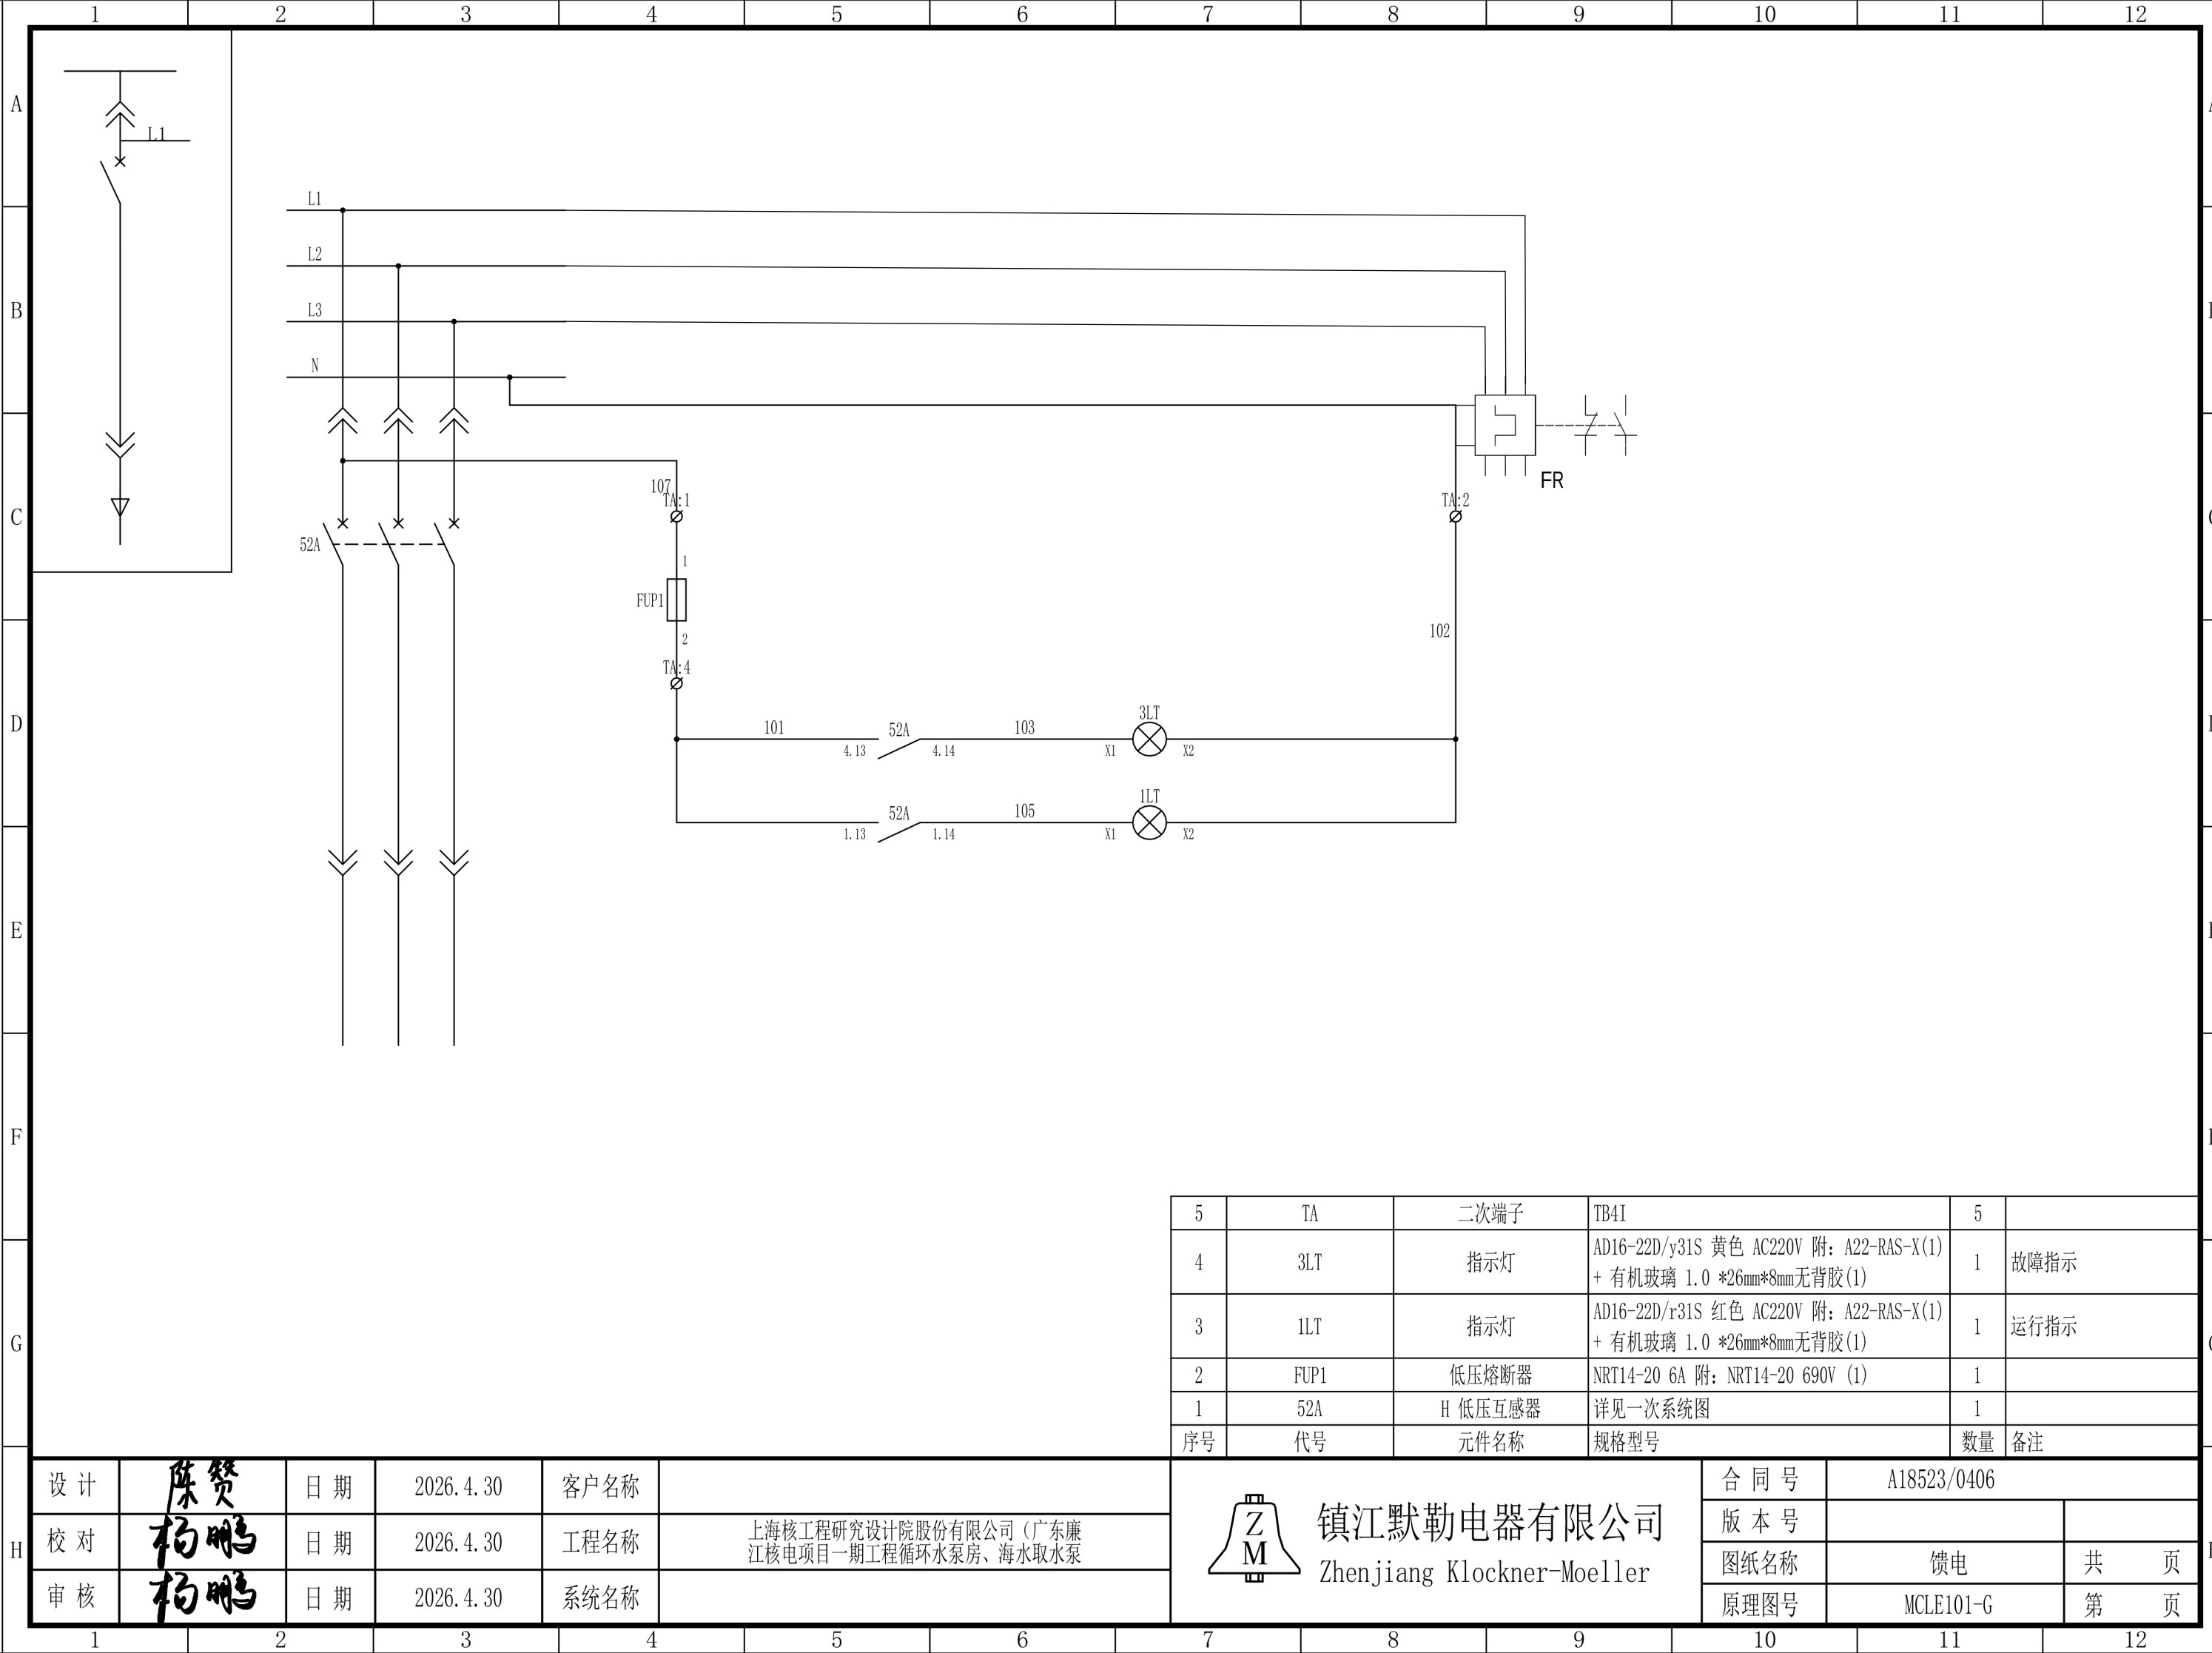

5	TA	二次端子	TB4I	5	
4	3LT	指示灯	AD16-22D/y31S 黄色 AC220V 附: A22-RAS-X(1) + 有机玻璃 1.0 *26mm*8mm无背胶(1)	1	故障指示
3	1LT	指示灯	AD16-22D/r31S 红色 AC220V 附: A22-RAS-X(1) + 有机玻璃 1.0 *26mm*8mm无背胶(1)	1	运行指示
2	FUP1	低压熔断器	NRT14-20 6A 附: NRT14-20 690V (1)	1	
1	52A	H 低压互感器	详见一次系统图	1	
序号	代号	元件名称	规格型号	数量	备注

设计	陈赞	日期	2026. 4. 30	客户名称	
校对	杨鹏	日期	2026. 4. 30	工程名称	上海核工程研究设计院股份有限公司 (广东廉江核电项目一期工程循环水泵房、海水取水泵)
审核	杨鹏	日期	2026. 4. 30	系统名称	

 镇江默勒电器有限公司 Zhenjiang Klockner-Moeller	合同号	A18523/0406	
	版本号		
	图纸名称	馈电	共 页
	原理图号	MCLE101-G	第 页