



A
B
C
D
E
F
G
H

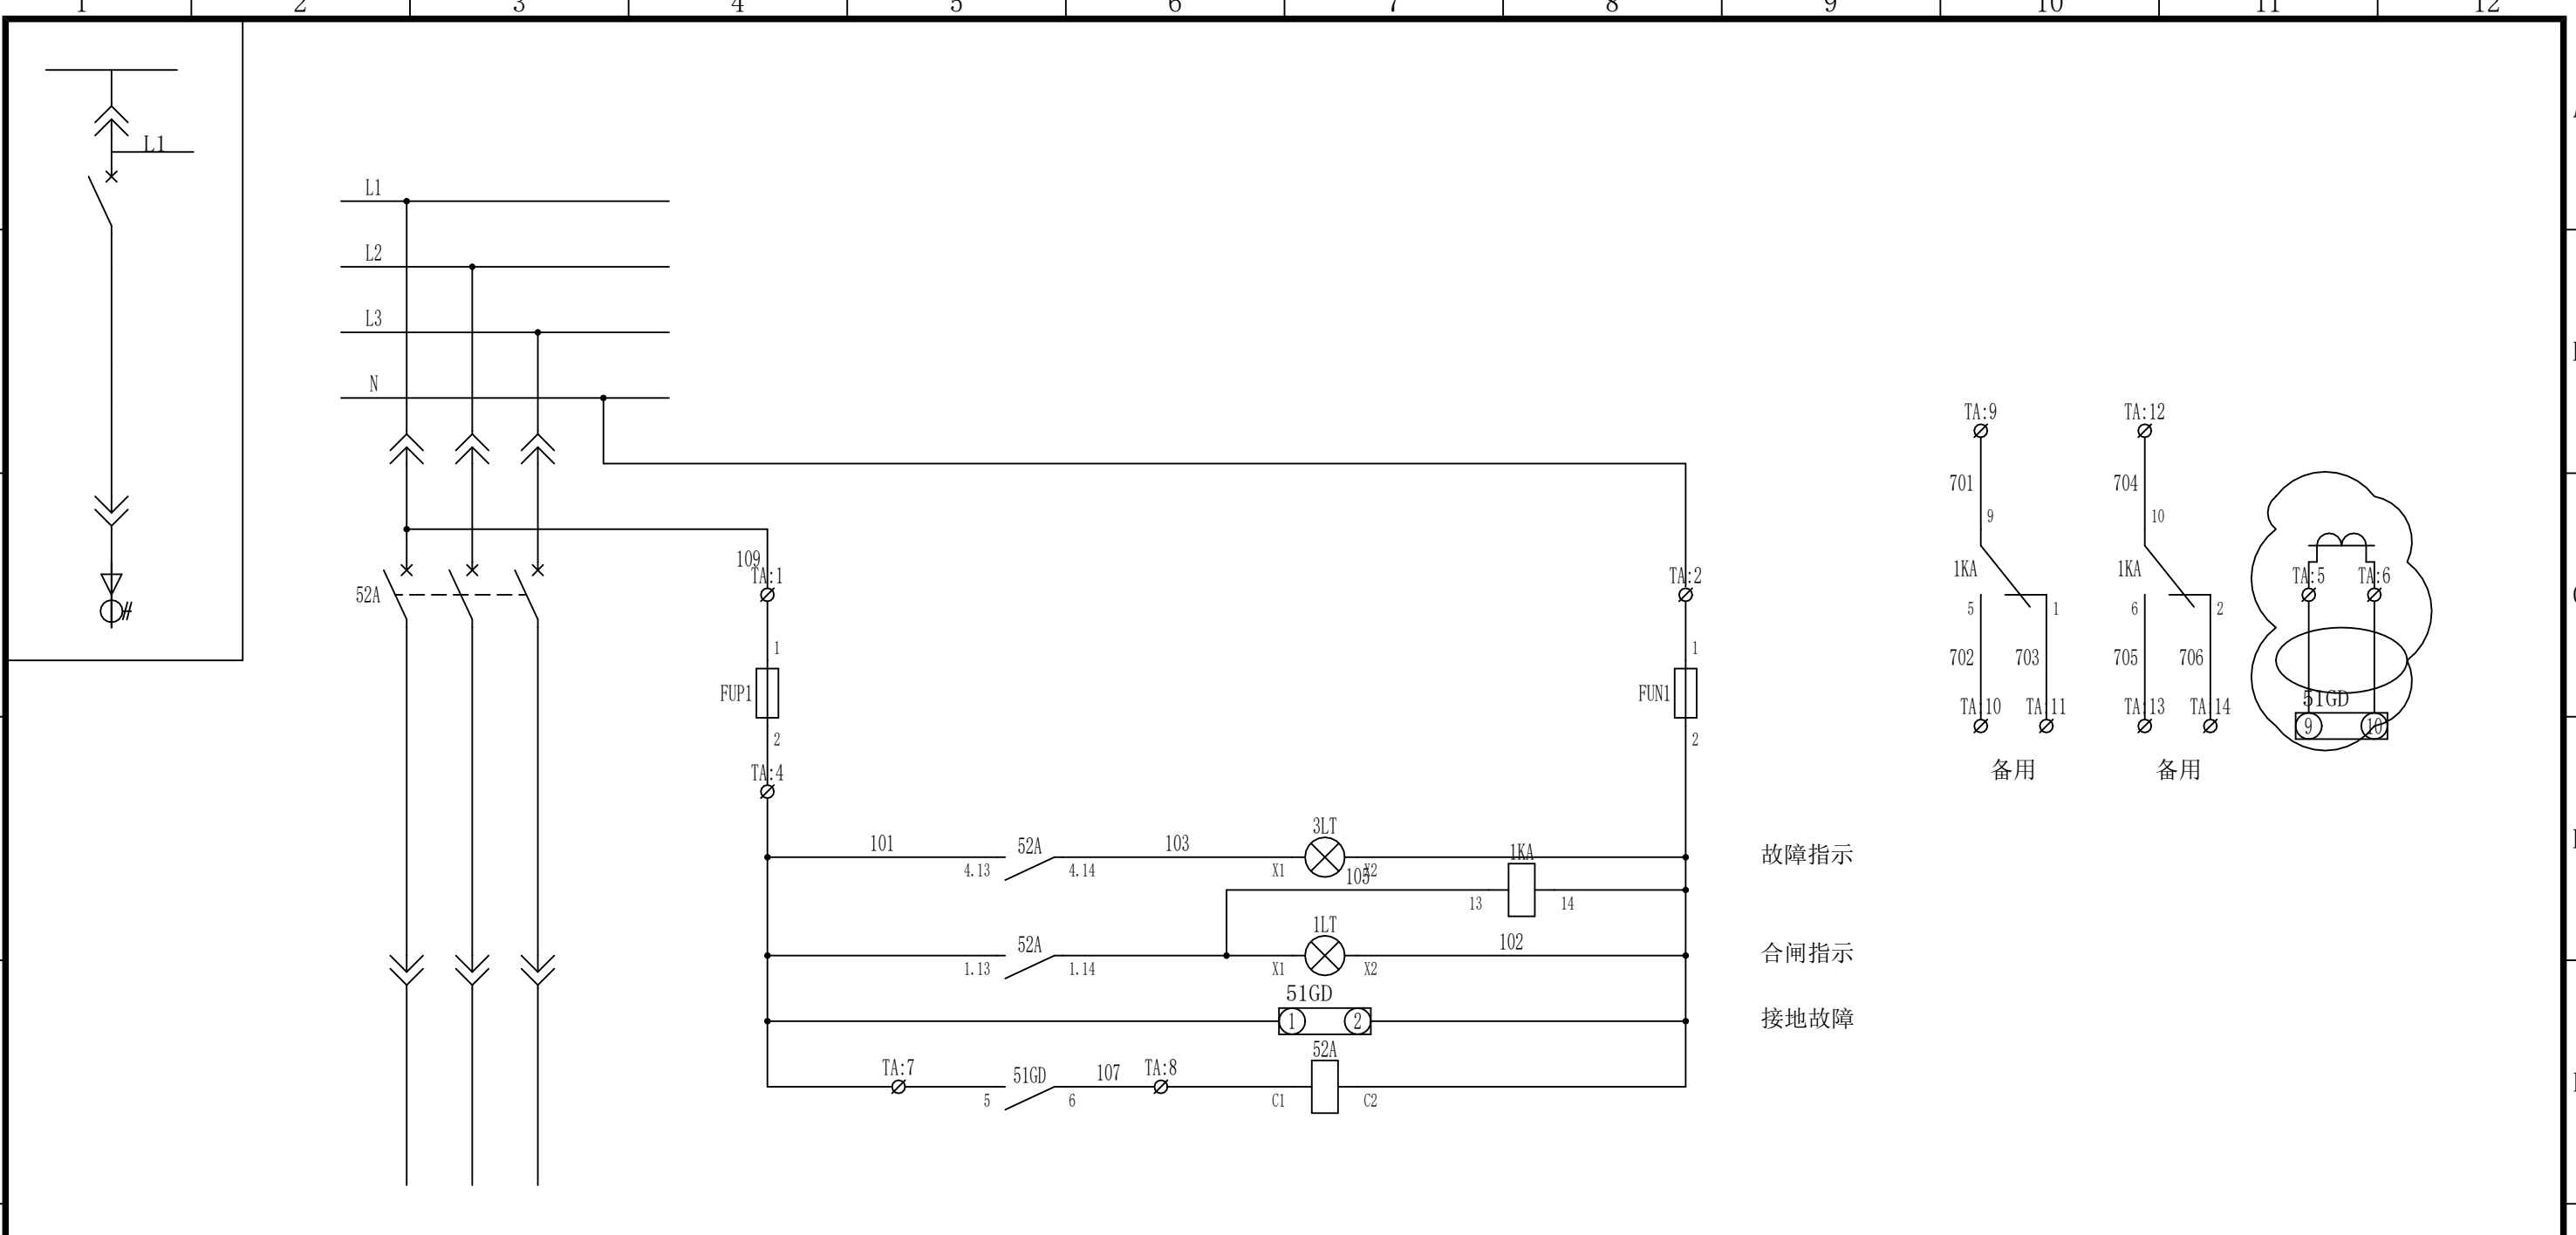

装置有接
地要接地

8	TA_附件	端子（附件）	D-TB4/10 附：E/UK（2）+ UZB6横 1-10（1）	1	
7	TA	二次端子	TB4I	16	
6	3LT	指示灯	AD16-22D/y31S 黄色 AC220V 附：A22-RAS-X(1) + 有机玻璃 1.0 *26mm*8mm无背胶(1)	1	故障指示
5	1LT	指示灯	AD16-22D/r31S 红色 AC220V 附：A22-RAS-X(1) + 有机玻璃 1.0 *26mm*8mm无背胶(1)	1	运行指示
4	FUN1, FUP1	低压熔断器	NRT14-20 6A 附：NRT14-20 690V（1）	2	
3	1KA	继电器	CR-MX230AC4 附：CR-M4SS10095969(1) + CR-MH1(2)	1	
2	51GD	H火灾监控	详见一次系统图	1	
1	52A	S 塑壳断路器	详见一次系统图	1	
序号	代号	元件名称	规格型号	数量	备注

设计	陈赞	日期	2026. 4. 30	客户名称	
校对	杨鹏	日期	2026. 4. 30	工程名称	上海核工程研究设计院股份有限公司（广东廉江核电项目一期工程循环水泵房、海水取水泵
审核	杨鹏	日期	2026. 4. 30	系统名称	

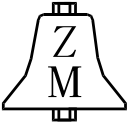

镇江默勒电器有限公司
Zhenjiang Klockner-Moeller

合同号	A18523/0406	
版本号		
图纸名称	馈电带零序	共 页
原理图号	MCLE102-G	第 页