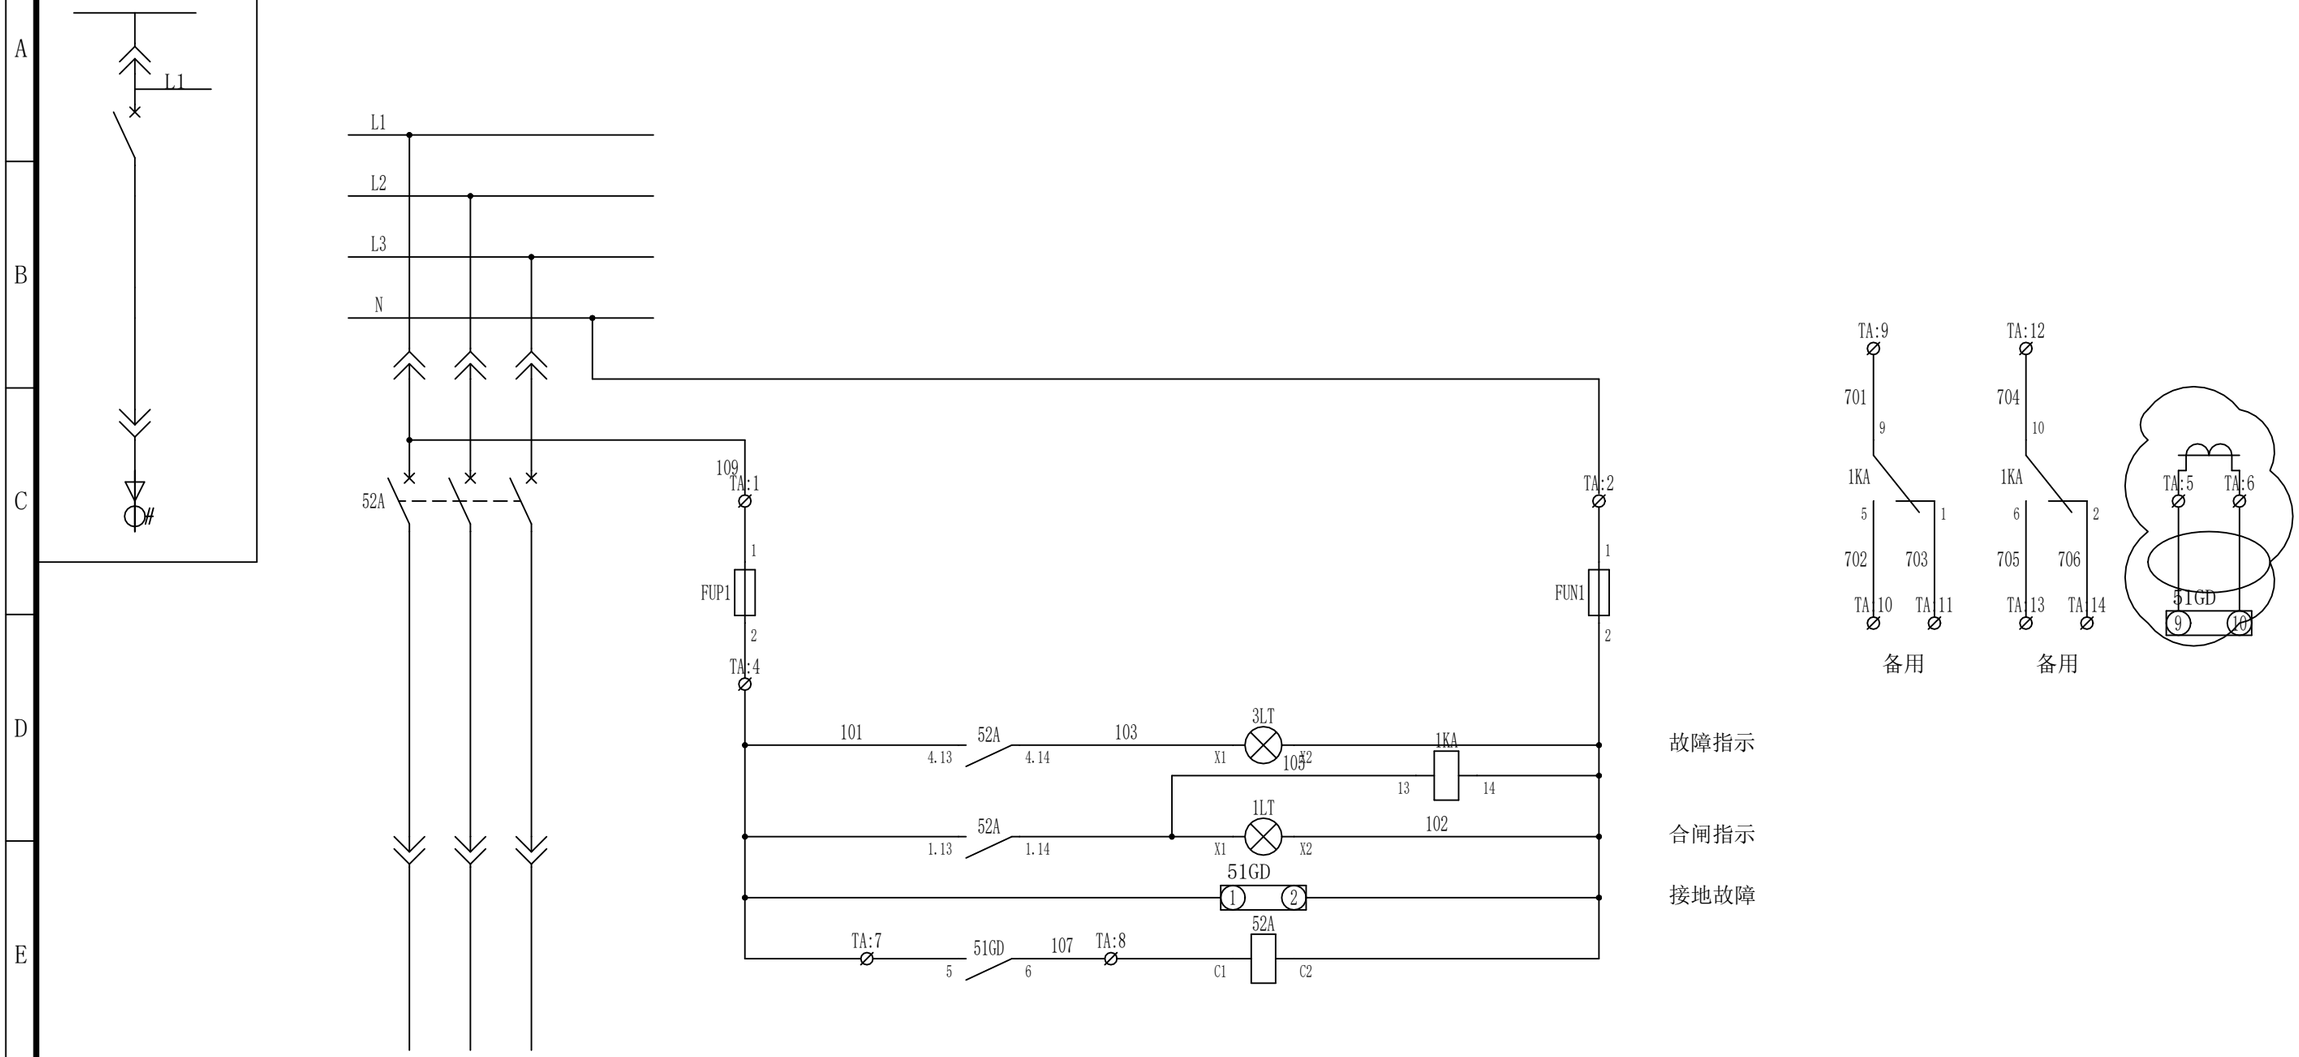

8	TA_附件	端子（附件）	D-TB4/10　附：E/UK (2) + UZB6横 1-10 (1)	1	
7	TA	二次端子	TB4I	16	
6	3LT	指示灯	HD-22DL/AC220VY 附：A22-RAS-X(1) + 有机玻璃 1.0 *26mm*8mm无背胶(1)	1	故障指示
5	1LT	指示灯	HD-22DL/AC220VR 附：A22-RAS-X(1) + 有机玻璃 1.0 *26mm*8mm无背胶(1)	1	运行指示
4	FUN1,FUP1	低压熔断器	NRT14-20 6A 附：NRT14-20 690V (1)	2	
3	1KA	继电器	CR-MX230AC4 附：CR-M4SS10095969(1) + CR-MH1(2)	1	
2	51GD	H火灾监控	详见一次系统图	1	
1	52A	S 塑壳断路器	详见一次系统图	1	
序号	代号	元件名称	规格型号	数量	备注

设 计	陈赟	日 期	2025.12.24	客户名称	
校 对	江彬	日 期	2025.12.24	工程名称	上海核工程研究设计院股份有限公司（广东廉江清洁能源项目海水取水泵房、循环水泵房项
审 核	杨鹏	日 期	2025.12.24	系统名称	

镇江默勒电器有限公司
Zhenjiang Klockner-Moeller

合 同 号	A19996/0206	
版 本 号		
图纸名称	馈电带零序	共　页
原理图号	MCLE102-G	第　页