
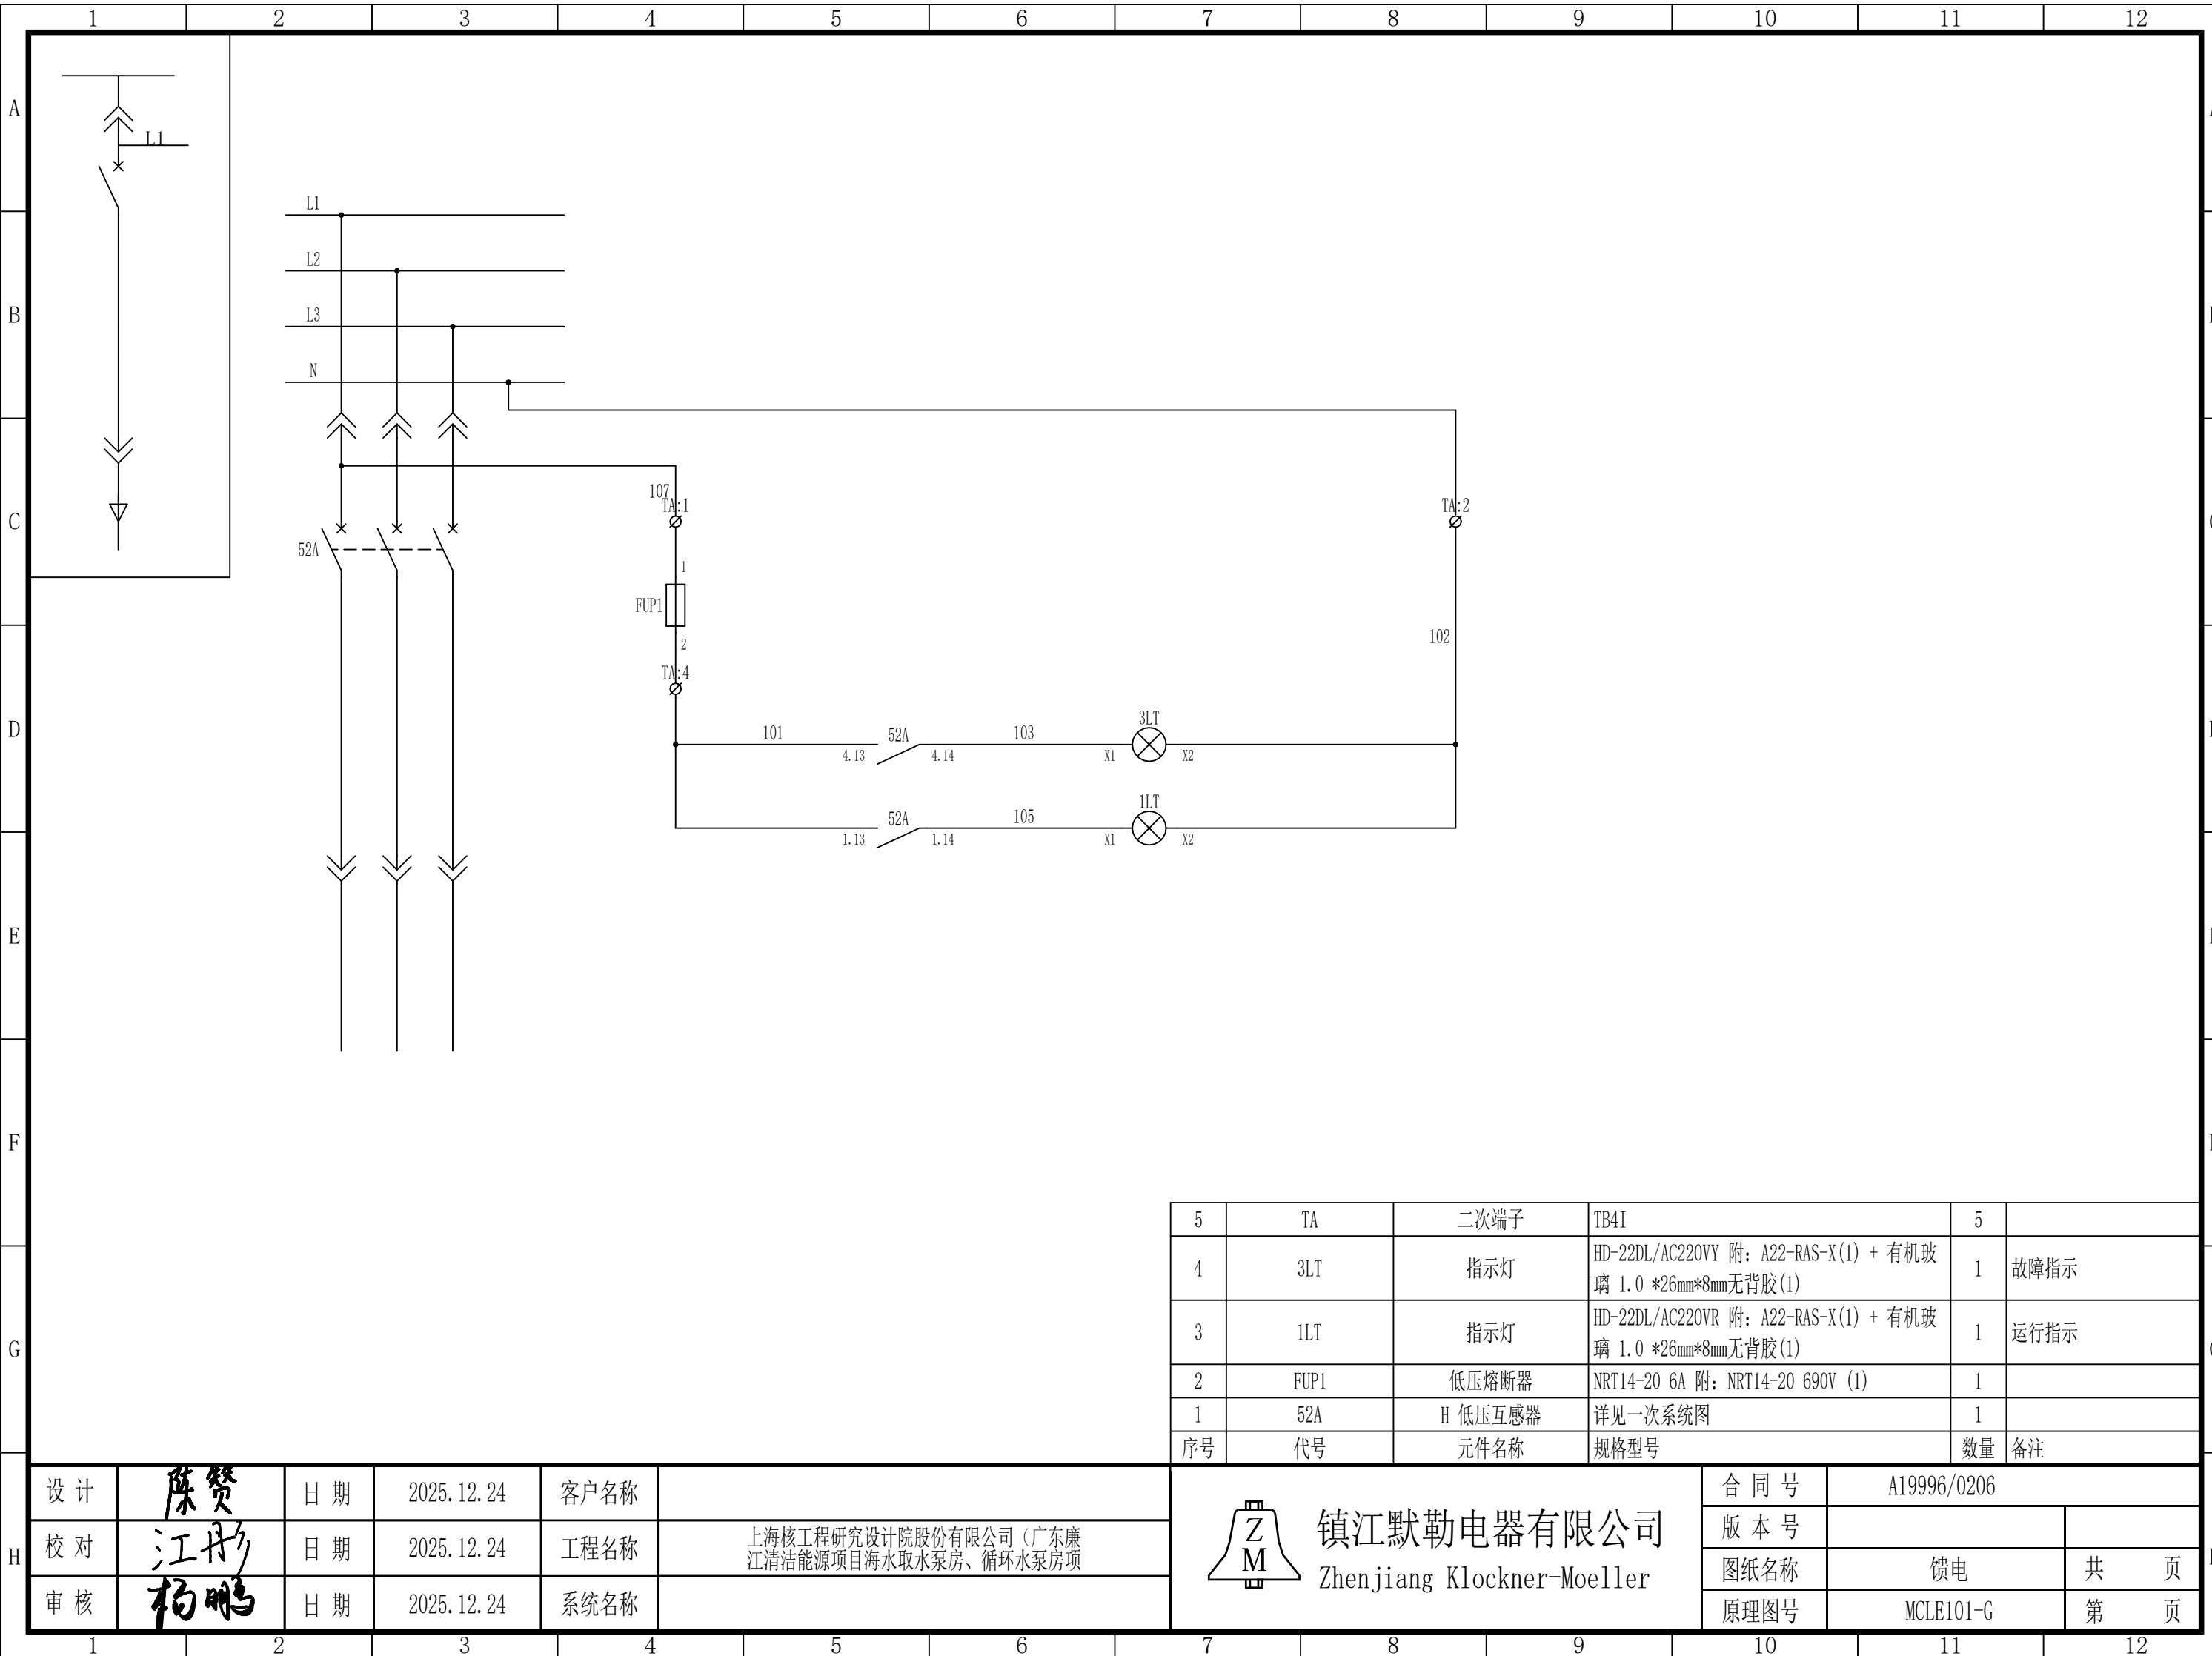


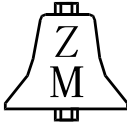

设计	陈赞	日期	2025.12.24	客户名称	
校对	江彤	日期	2025.12.24	工程名称	上海核工程研究设计院股份有限公司（广东廉江清洁能源项目海水取水泵房、循环水泵房项
审核	杨鹏	日期	2025.12.24	系统名称	

	镇江默勒电器有限公司		合同号	A19996/0206	
	Zhenjiang Klockner-Moeller		版本号		
			图纸名称	馈电	共 页
			原理图号	MCLE101-G	第 页