
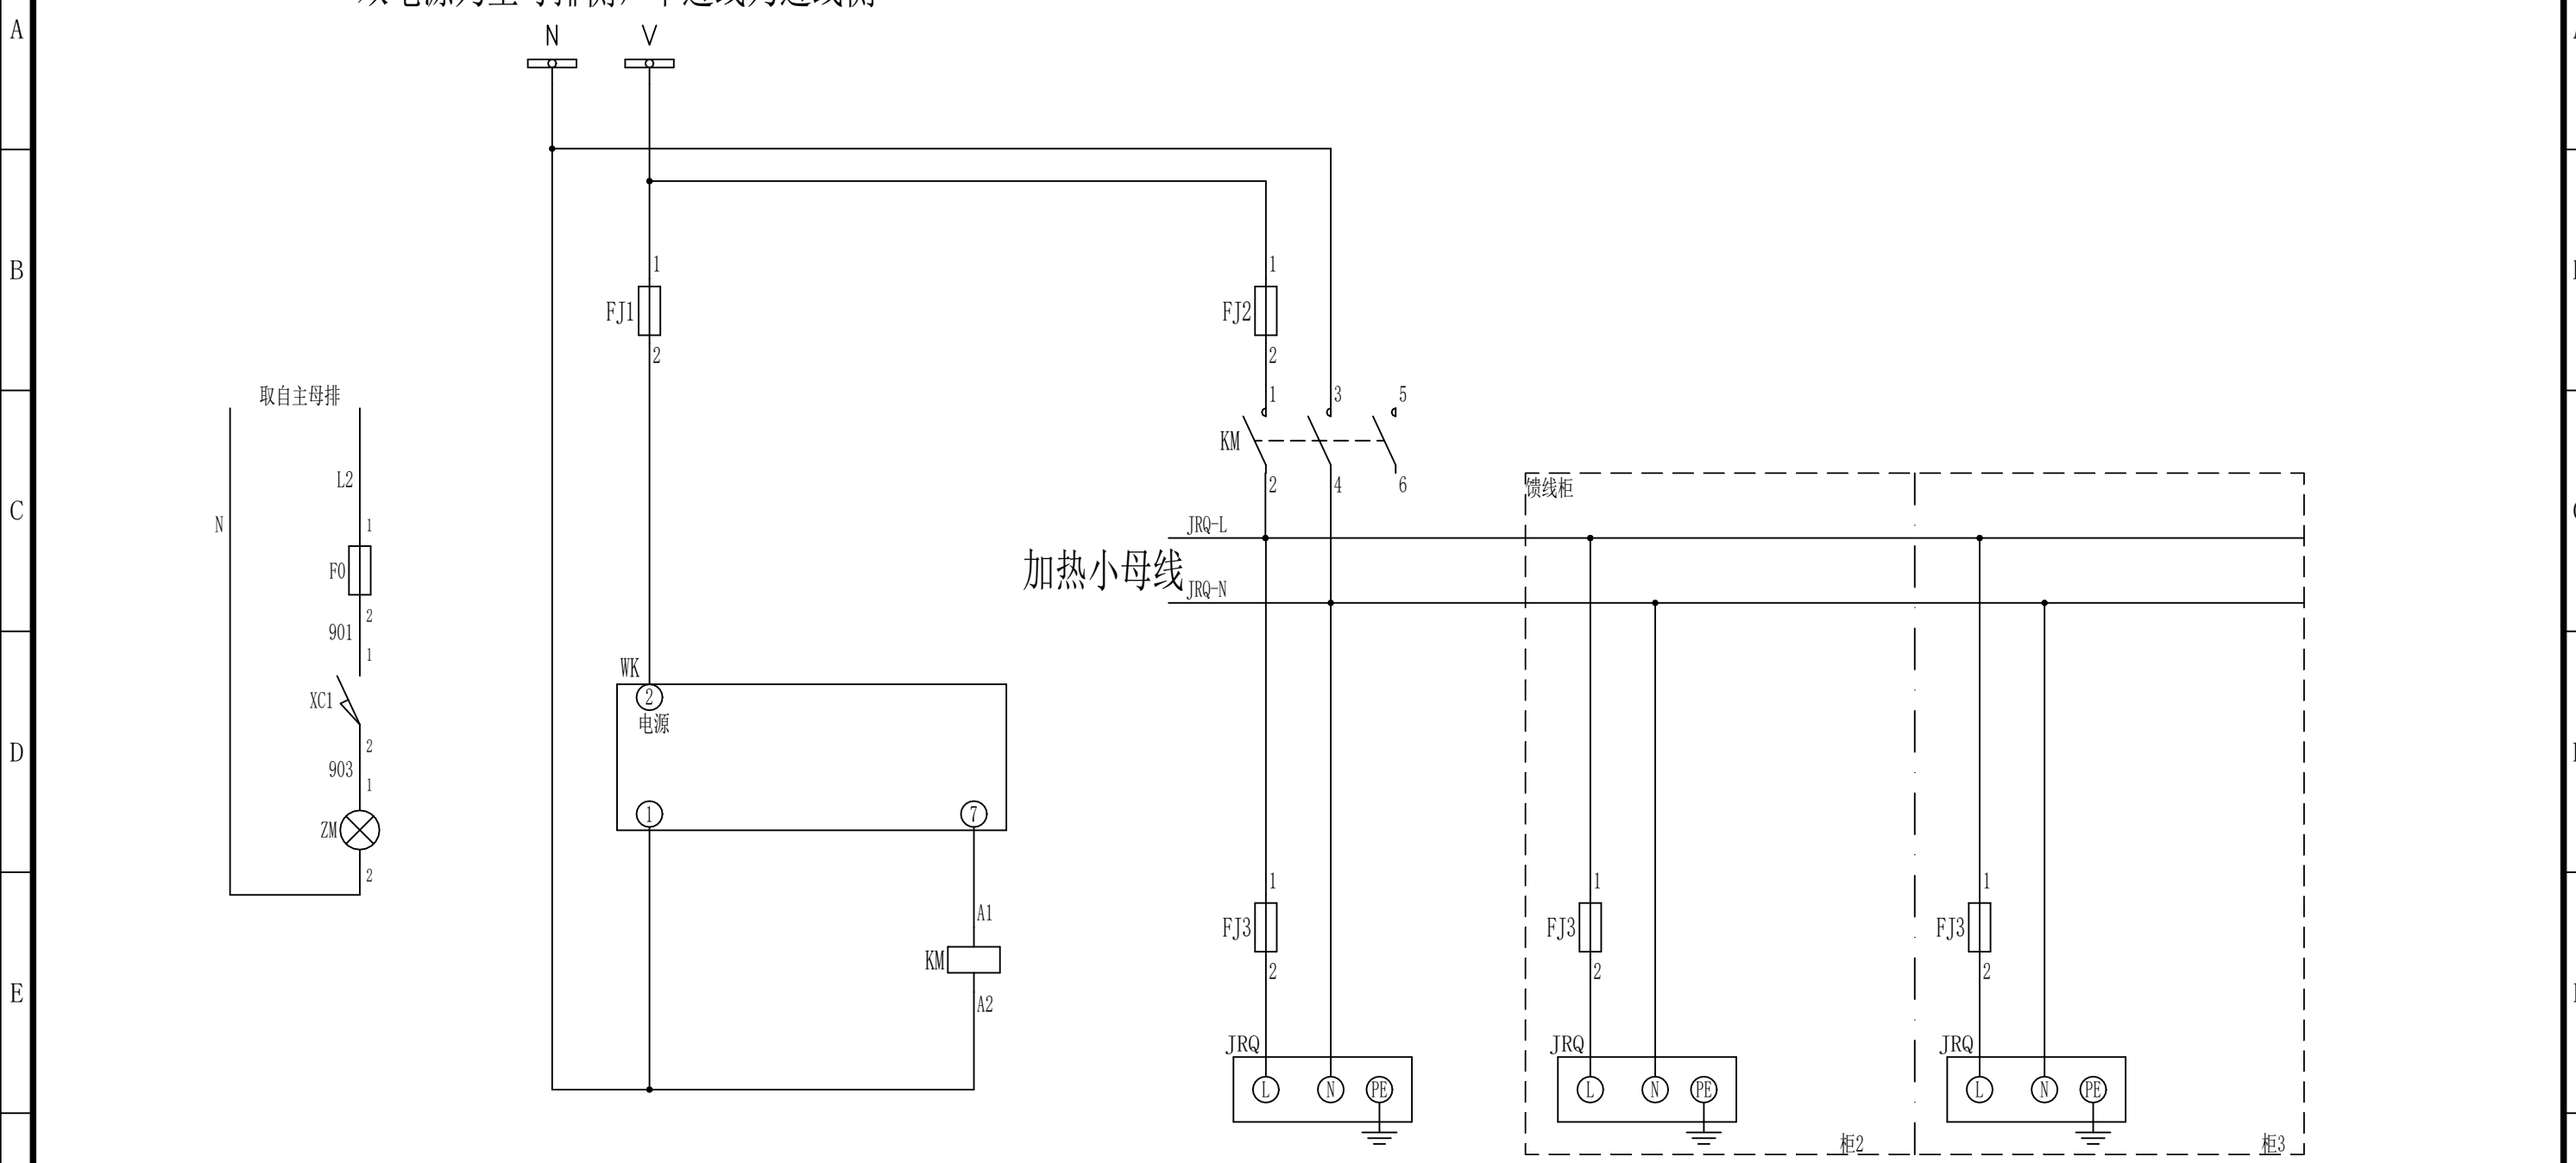


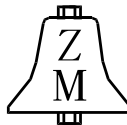

8	ZM	照明灯	T5-15 LED灯	1	
7	XC1	行程开关	JW2-11H/L	1	
6	小母线	一次端子	ZPDB 10/4X6/J10	2	
5	WK	温湿度控制器	DQY-TH200-4X/D1WSS 装置AC/DC80~275V	1	
4	KM	接触器	3RT6016-1AN21 (9A)	1	
3	JRQ	加热器	DJR11-100W AC230V	1	
2	FJ2	低压熔断器	NRT14-20 10A 附: NRT14-20 690V (1)	1	
1	FJ1, FJ3, F0	低压熔断器	NRT14-20 6A 附: NRT14-20 690V (1)	3	
序号	代号	元件名称	规格型号	数量	备注

H	设计	赵青	日期	2025.8	客户名称	 镇江默勒电器有限公司 Zhenjiang Klockner-Moeller	合同号		
	校对	陶梓明	日期	2025.8	工程名称		版本号		
	审核	杨鹏	日期	2025.8	系统名称		图纸名称	温湿度控制器+加热器	共 1 页
							原理图号	TYPE-WKJRQ	第 1 页